
SOUTH FLORIDA, FL
FIRE DAMAGE REPAIR
DUPLEX
MULTI-FAMILY

LOCATION MAP REMOVED

Property Information
Owner Name : WITHHELD
Parcel Control Number : WITHHELD
Location Address : WITHHELD
Structural Details
Structural Element for Building 1
Bldg Type DUPLEX
Exterior Wall 1 MSY: CONC. BLOCK
Year Built 1960
Air Condition Desc. NO HTG/AC
Heat Type NONE
Heat Fuel NONE
Bed Rooms 2
Full Baths 2
Half Baths 0
Exterior Wall 2 NONE
Roof Structure FLAT
Roof Cover ROLLED COMPOSITION
Interior Wall 1 PLASTER
Interior Wall 2 N/A
Floor Type 1 CARPETING
Stories 1
Subarea and Square Footage for Building 1
Code Description square Footage
BAS Base Area 1320
Total Square Footage 1320
Area Under Air 1320

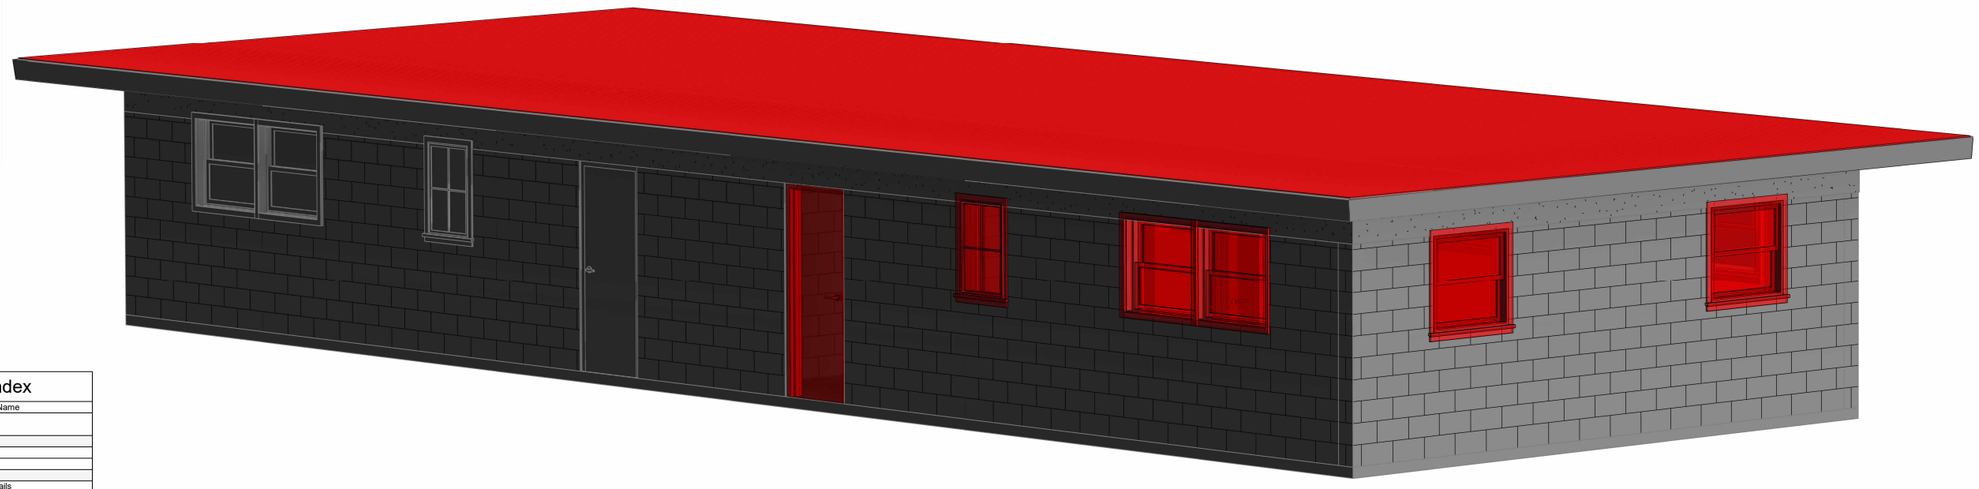

Structural Sheet Index

Sheet Number	Sheet Name
General	
G100	Cover
Structural	
S101	Floor Plans
S102	Demolition Floor Plans
S103	Demolition Sections & Details
S104	Existing Roof Framing Plan -Demolition
S105	Demolition Elevations
S106	Repair Floor Plans
S107	Repair Roof Plan
S108	Repair Elevations
S109	Repair Sections & Details
S110	Window & Detail Sections
Mechanical	
M101	Mechanical Plans
M102	Mechanical Notes & Specs
Electrical	
E101	Electrical Plans
E102	Electrical Schedules
E103	Electrcial Notes & Specs

WWW.RANSOMSOLUTION.COM

CONFIDENTIAL CLIENT

SOUTH FLORIDA, FL

PORTFOLIO SAMPLE - CLIENT INFORMATION REMOVED

FIRE DAMAGE REPAIR

No.	Description	Date

Cover

Project number	RS-1053
Date	09/04/26
Drawn by	S.B.R.
Checked by	
Scale	NOT TO SCALE

G100

SEAL REMOVED
PORTFOLIO SAMPLE

ENGINEER SEAL

Project Location:
SOUTH FLORIDA, FL

LOCATION MAP REMOVED

GENERAL NOTES

1. THESE DOCUMENTS ARE DESCRIPTIVE IN NATURE AND REPRESENT THE MINIMUM REQUIREMENTS NECESSARY TO COMPLY WITH ALL APPLICABLE CODES AND TO PROPERLY CONSTRUCT THE WORK. WORK NOT SPECIFICALLY SHOWN OR NOTED, BUT REQUIRED FOR A COMPLETE AND CODE-COMPLIANT INSTALLATION, SHALL BE INCLUDED. CONDITIONS NOT DETAILED SHALL BE EXECUTED IN A MANNER CONSISTENT WITH THE INTENT AND QUALITY OF THE PROJECT.
2. THIS PLAN SET IS SUBMITTED FOR A DEMOLITION & REPAIR PERMIT TO ADDRESS FIRE DAMAGE TO THE EAST UNIT OF THE DUPLEX. THERE WAS NO DAMAGE REPORTED NOR OBSERVED TO THE WEST UNIT AS A RESULT OF THE FIRE. . SCOPE INCLUDES DEMOLITION OF THE FIRE DAMAGED STRUCTURE AND REPAIR. REPAIR SCOPE INCLUDES WOOD ROOF FRAMING, BLOCKING, NEW WINDOWS & DOORS, NEW PLUMBING, ELECTRICAL, AND MECHANICAL. HATCHED AREAS ON PLANS INDICATE THE AREA OF DEMOLITION.
3. THE EXISTING DUPLEX WAS ORIGINALLY CONSTRUCTED CIRCA 1960. FIRE DAMAGE AND SUBSEQUENT DEMOLITION ACTIVITIES HAVE EXPOSED VOIDS AT THE INTERSECTION OF THE DEMISING WALL AND ROOF FRAMING. RECONSTRUCTION SHALL INCLUDE RESTORATION OF FIREBLOCKING AND CLOSURE OF CONCEALED OPENINGS AT THE OF THE DEMISING WALL UTILIZING MINERAL WOOL FIRE SAFING AND FIRE-RESISTANT SEALANT TO RESTORE THE SEPARATION BETWEEN DWELLING UNITS STRUCTURAL FRAMING EXPOSED DURING DEMOLITION SHALL BE EVALUATED AND REPAIRED OR REPLACED AS REQUIRED BASED UPON OBSERVED FIELD CONDITIONS ALL WORK AND MATERIALS SHALL COMPLY WITH THE FLORIDA BUILDING CODE (FBC), 2023 EDITION, AND APPLICABLE REFERENCED STANDARDS. THESE PLANS WERE PREPARED IN ACCORDANCE WITH ALL APPLICABLE BUILDING CODES INCLUDING FBC 2023.
4. EXISTING DIMENSIONS ARE PROVIDED FOR REFERENCE ONLY. CONTRACTOR SHALL FIELD VERIFY ALL EXISTING CONDITIONS AND DIMENSIONS PRIOR TO DEMOLITION. DO NOT SCALE DRAWINGS.
5. EXISTING BUILDING COMPONENTS DESIGNATED TO REMAIN SHALL BE THOROUGHLY INSPECTED, CLEANED, AND RESTORED FOLLOWING FIRE, SMOKE, SOOT, AND HEAT EXPOSURE. REPLACE COMPONENTS THAT CANNOT BE ADEQUATELY CLEANED, RESTORED, OR DEMONSTRATED TO BE STRUCTURALLY AND FUNCTIONALLY SOUND.
6. REMOVE ALL VISIBLE SOOT, SMOKE RESIDUE, AND FIRE-RELATED DEPOSITS FROM EXISTING SURFACES TO REMAIN USING CLEANING METHODS AND PRODUCT APPROPRIATE FOR THE SUBSTRATE AND MANUFACTURER'S RECOMMENDATIONS. DO NOT CONCEAL OR ENCAPSULATE SOOT OR SMOKE RESIDUE PRIOR TO CLEANING.
7. EXISTING PAINTED SURFACES EXHIBITING SOOT STAINING SHALL BE CLEANED AND EVALUATED AFTER CLEANING. SURFACES SHALL BE PREPARED AS REQUIRED PRIOR TO REPAINTING, INCLUDING REMOVAL OF LOOSE, BLISTERED, PEELING, OR OTHERWISE UNSOUND COATINGS.
8. EXISTING PAINTED OR COATED SURFACES EXHIBITING ALLIGATORING, CRAZING, BLISTERING, WRINKLING, CRACKING, PEELING, OR OTHER COATING DISTRESS SHALL BE EVALUATED. REMOVE ALL LOOSE OR POORLY BONDED COATING. WHERE DISTRESS IS EXTENSIVE OR THE UNDERLYING SUBSTRATE HAS BEEN AFFECTED, REMOVE THE EXISTING COATING TO A SOUND SUBSTRATE AND REFINISH.
9. COATINGS EXHIBITING EVIDENCE OF HEAT DAMAGE, INCLUDING DISCOLORATION, BLISTERING, BUBBLING, WRINKLING, ALLIGATORING, LOSS OF ADHESION, OR OTHER DEFORMATION, SHALL NOT BE PAINTED OVER. REMOVE AFFECTED COATINGS AND INSPECT THE SUBSTRATE FOR ADDITIONAL DAMAGE.
10. CONTRACTOR SHALL MAINTAIN THE PROPERTY IN A WEATHER-TIGHT CONDITION DURING CONSTRUCTION AND SHALL PROTECT THE EXISTING STRUCTURE FROM WATER INTRUSION.
11. THE CONTRACTOR SHALL FURNISH AND BE SOLELY RESPONSIBLE FOR ALL TEMPORARY BRACING AND SHORING REQUIRED TO MAINTAIN PLUMBNESS AND STABILITY OF ALL STRUCTURAL ELEMENTS DURING CONSTRUCTION AND WHEN DEMOLITION AFFECTS SHARED LOAD-BEARING WALLS, ROOF FRAMING, OR COMMON STRUCTURAL ELEMENTS.
12. EXISTING UTILITIES SERVING THE DAMAGED UNIT SHALL BE DISCONNECTED, CAPPED, AND SECURED PRIOR TO DEMOLITION. UTILITIES SERVING THE ADJACENT UNIT SHALL REMAIN OPERATIONAL UNLESS OTHERWISE NOTED (UON).
13. CONTRACTOR SHALL PATCH AND REPAIR ALL WORK DISTURBED BY THE DEMOLITION TO MATCH ADJOINING FINISHES.
14. THE CONTRACTOR SHALL REMOVE ALL CONSTRUCTION DEBRIS ON A DAILY BASIS AND MAINTAIN A CLEAN ORGANIZED CONSTRUCTION SITE THROUGHOUT THE DURATION OF THE WORK.
15. IF ANY MISTAKES, OMISSIONS, OR DISCREPANCIES ARE FOUND IN THE PLANS, THE DESIGN PROFESSIONALS SHALL BE PROMPTLY NOTIFIED SO THERE WILL BE THE OPPORTUNITY FOR THEM TO REMEDY THE PROBLEM. ACTIONS TAKEN WITHOUT THE KNOWLEDGE AND CONSENT OF THE ENGINEER SHALL BECOME THE RESPONSIBILITY OF THOSE PARTIES TAKING SUCH ACTIONS.
16. ALL APPROVED SHOP DRAWINGS SHALL BE REVIEWED BY THE EOR AND SUBMITTED AND PROCESSED AT THE LOCAL BUILDING DEPARTMENT
17. UNLESS OTHERWISE INDICATED IN THE CONTRACT DOCUMENTS THE CONTRACTOR IS SOLELY RESPONSIBLE FOR HIS MEANS, METHODS, TOOLS,SCHEDULING, AND COORDINATION IN THE CONSTRUCTION OF THE WORKS.

SITE INFORMATION
WITHHELD
Municipality
WITHHELD
Parcel No.
WITHHELD
Subdivision
WITHHELD

Use Type
0800 - MULTIFAMILY < 5 UNITS
Total Square Feet
1320

GENERAL CONSTRUCTION NOTES:
1. CONTRACTOR SHALL PROPERLY PATCH AND REPAIR ALL WORK DISTURBED BECAUSE OF THE ALTERATION AND IS TO MATCH ALL ADJOINING WORK. PROVIDE R-5 FOIL BACK INSULATION AT EXTERIOR WALLS.
2. PROVIDE 1x2 FURRING STRIPS AT 16" C.C WITH (1) CUT NAIL EVERY COURSE OF MASONRY WALL. EXTERIOR WALLS: APPLY STUCCO AND PAINT TO MATCH EXISTING ADJACENT AREAS
3. ALL PARTITIONS SHALL BE METAL STUDS AT 16" C.C 25 GAUGE MIN.
4. INTERIOR WALLS: APPLY 1/2" DRYWALL, PLASTER AND PAINT TO MATCH EXISTING ADJACENT AREAS.
5. HOLD ALL ROUGH OPENINGS FOR DOORS 4" FROM FACE OF ADJACENT FINISHED WALL.
6. FINAL LOCATION OF ALL EQUIPMENT, RECEPTACLES, ETC. ARE SUBJECT TO REASONABLE CHANGES IN THE LOCATION UP TO ROUGHING-IN.

WOOD NOTES
1. ALL LUMBER SHALL BE NO. 2 OR BETTER SOUTHERN PINE.
2. 1x6 NOMINAL TONGUE AND GROOVE (T&G) WOOD SHEATHING TO MATCH EXISTING SIZE, SPECIES, GRADE, AND THICKNESS, UON.
3. ALL FASTENERS SHALL BE HOT-DIPPED GALVANIZED OR STAINLESS STEEL.

DOORS & WINDOWS NOTES:
1. ALL DOOR AND WINDOW OPENINGS SHALL BE INSTALLED PER MANUFACTURER'S SPECIFICATIONS.
2. ALL ROUGH OPENINGS MUST BE VERIFIED BY THE CONTRACTOR PRIOR TO CONSTRUCTION. FIELD VERIFY ALL DIMENSIONS PRIOR TO FABRICATION.
3. NEW DOORS AND WINDOWS SHALL BE SCHEDULE ON THESE DRAWINGS.
4. 2x PT BUCKS/NAILERS SHALL EXTEND BEYOND INTERIOR FACE OF WINDOW.

METAL WALL FRAMING:
1. STEEL STUDS AND RUNNERS USED TO CONSTRUCT FIRE RESISTIVE WALLS OR PARTITIONS SHALL BE DIPPED GALVANIZED IN ACCORDANCE WITH ASTM A525 , COATING DESIGNATION G40 MINIMUM; AND BE OF CHANNEL OR "C" TYPE SHAPE. THE TOTAL THICKNESS OF THE BASE METAL PLUS COATING SHALL NOT BE LESS THAN 0.0184" UNPAINTED AND NOT LESS THAN 0.0194" IF COATED AND PAINTED. STUDS AND RUNNERS SHALL COMPLY WITH ASTM C645 AND HAVE A BASE METAL THICKNESS BEFORE APPLICATION OF ANY COATING, OF NOT LESS THAN 0.0179". STEEL STUDS AND RUNNERS USED IN PARTITIONS NEED NOT BE GALVANIZED, BUT MUST MEET ALL OTHER REQUIREMENTS AND SHALL COMPLY WITH ASTM C525.
2. STEEL STUDS SUPPORTING WALL HUNG PLUMBING FIXTURES OR CABINETS SHALL BE DOUBLED OR NOT LESS THAN 20 GAUGE. SUCH STUDS SHALL BE RIGIDLY CONNECTED TOP AND BOTTOM TO PREVENT SIGNIFICANT END ROTATION OR DISPLACEMENT.
3. A HORIZONTAL MEMBER SECURELY FASTENED TO NOT LESS THAN TWO STUDS SHALL BE INSTALLED FOR THE ATTACHMENT OF EACH WALL HUNG PLUMBING FIXTURE OR CABINET.
4. RUNNERS SHALL BE FASTENED TO THE CEILING, CONTIGUOUS WALLS, AND PARTITIONS, AND TO THE FLOOR AT INTERVALS NOT EXCEEDING 24" ON CENTER.


DESIGN CRITERIA
DESIGN LOADS:

THE STRUCTURAL SYSTEM FOR THE ATTACHED DRAWINGS WERE DESIGNED PER THE WIND AND GRAVITY LOADING PRESENTED IN SECTION 16 OF THE FLORIDA BUILDING CODE, 2023 USING THE FOLLOWING SUPERIMPOSED.

DEAD LOAD	SELF-WEIGHT OF STRUCTURAL COMPONENTS
LIVE LOAD	30 PSF (ROOF)

WIND LOAD CRITERIA	
ULTIMATE WIND SPEED	168 MPH
NOMINAL WIND SPEED	130 MPH
IMPORTANCE FACTOR	1.0
BUILDING RISK CATEGORY	II
WIND EXPOSURE CATEGORY	B
ENCLOSURE CLASSIFICATION	ENCLOSED

IN THE EVENT OF CONFLICT BETWEEN PERTINENT CODES AND REGULATIONS AND THE REQUIREMENTS OF THE REFERENCED STANDARDS OF THESE SPECIFICATIONS THE PROVISIONS OF THE MORE STRINGENT SHALL GOVERN.

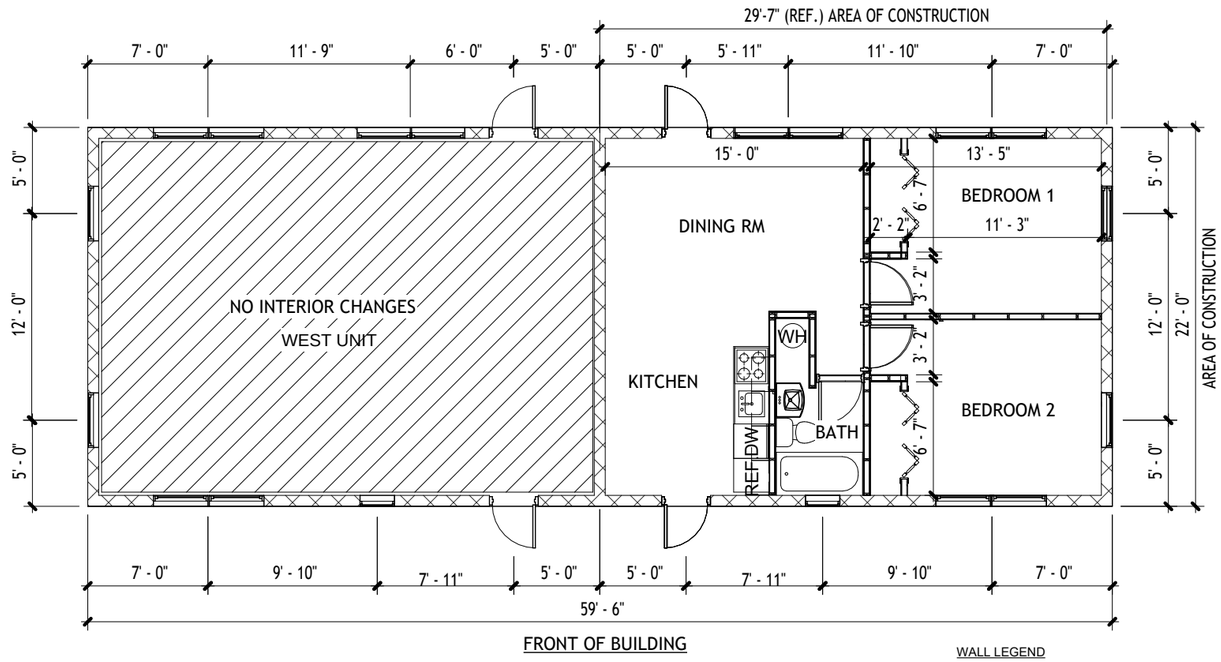

N

1 Existing Floor Plan - EAST UNIT
1/8" = 1'-0"

WALL LEGEND
- EXISTING 8" MASONRY WALL WITH PLASTER FINISH
- EXISTING 4" WOOD FRAMED INTERIOR WALL

ALL DIMENSIONS ARE FOR REFERENCE PURPOSES ONLY

WWW.RANSOMSOLUTION.COM

CONFIDENTIAL CLIENT

SOUTH FLORIDA, FL
PORTFOLIO SAMPLE - CLIENT INFORMATION REMOVED

FIRE DAMAGE REPAIR

No.	Description	Date

Floor Plans


Project number	RS-1053	S101
Date	09/04/26	
Drawn by	S.B.R.	
Checked by		Scale 1/8" = 1'-0"

SEAL REMOVED
PORTFOLIO SAMPLE

ENGINEER SEAL

DEMOLITION NOTES

1. PROVIDE TEMPORARY SHORING BENEATH EXISTING FIRE-EXPOSED ROOF GIRDER PRIOR TO COMMENCEMENT OF DEMOLITION. MAINTAIN SHORING UNTIL DEMOLITION IS COMPLETE AND EXISTING STRUCTURAL SUPPORT CONDITIONS HAVE BEEN VERIFIED BY THE EOR. TEMPORARY SHORING AND BRACING SHALL BE THE CONTRACTOR'S RESPONSIBILITY.
2. DEMOLITION SHALL BE LIMITED TO THE FIRE-DAMAGED DWELLING EAST UNIT AS INDICATED ON PLANS.
3. SHARED WALLS, COMMON ROOF FRAMING, FLOOR FRAMING, AND UTILITY SYSTEMS SHALL BE CAREFULLY EVALUATED IN THE FIELD PRIOR TO DEMOLITION. ANY STRUCTURAL MEMBERS INTENDED TO REMAIN SHALL BE PROTECTED FROM DAMAGE.
4. REMOVE ALL FIRE-DAMAGED MATERIALS INCLUDING, BUT NOT LIMITED TO, ROOFING, FRAMING, FINISHES, INSULATION WINDOWS, DOORS, MEP COMPONENTS WITHIN DEMOLITION LIMITS.
5. DEMOLITION SHALL CEASE IMMEDIATELY IF CONDITIONS ARE ENCOUNTERED THAT MAY COMPROMISE THE STABILITY OF THE REMAINING STRUCTURE.
6. ANY CONCEALED FIRE DAMAGE, STRUCTURAL DETERIORATION, ROT, INSECT DAMAGE, SPLITTING, OR EXCESSIVE CHARRING DISCOVERED DURING DEMOLITION SHALL BE REPORTED TO THE EOR PRIOR TO RECONSTRUCTION.

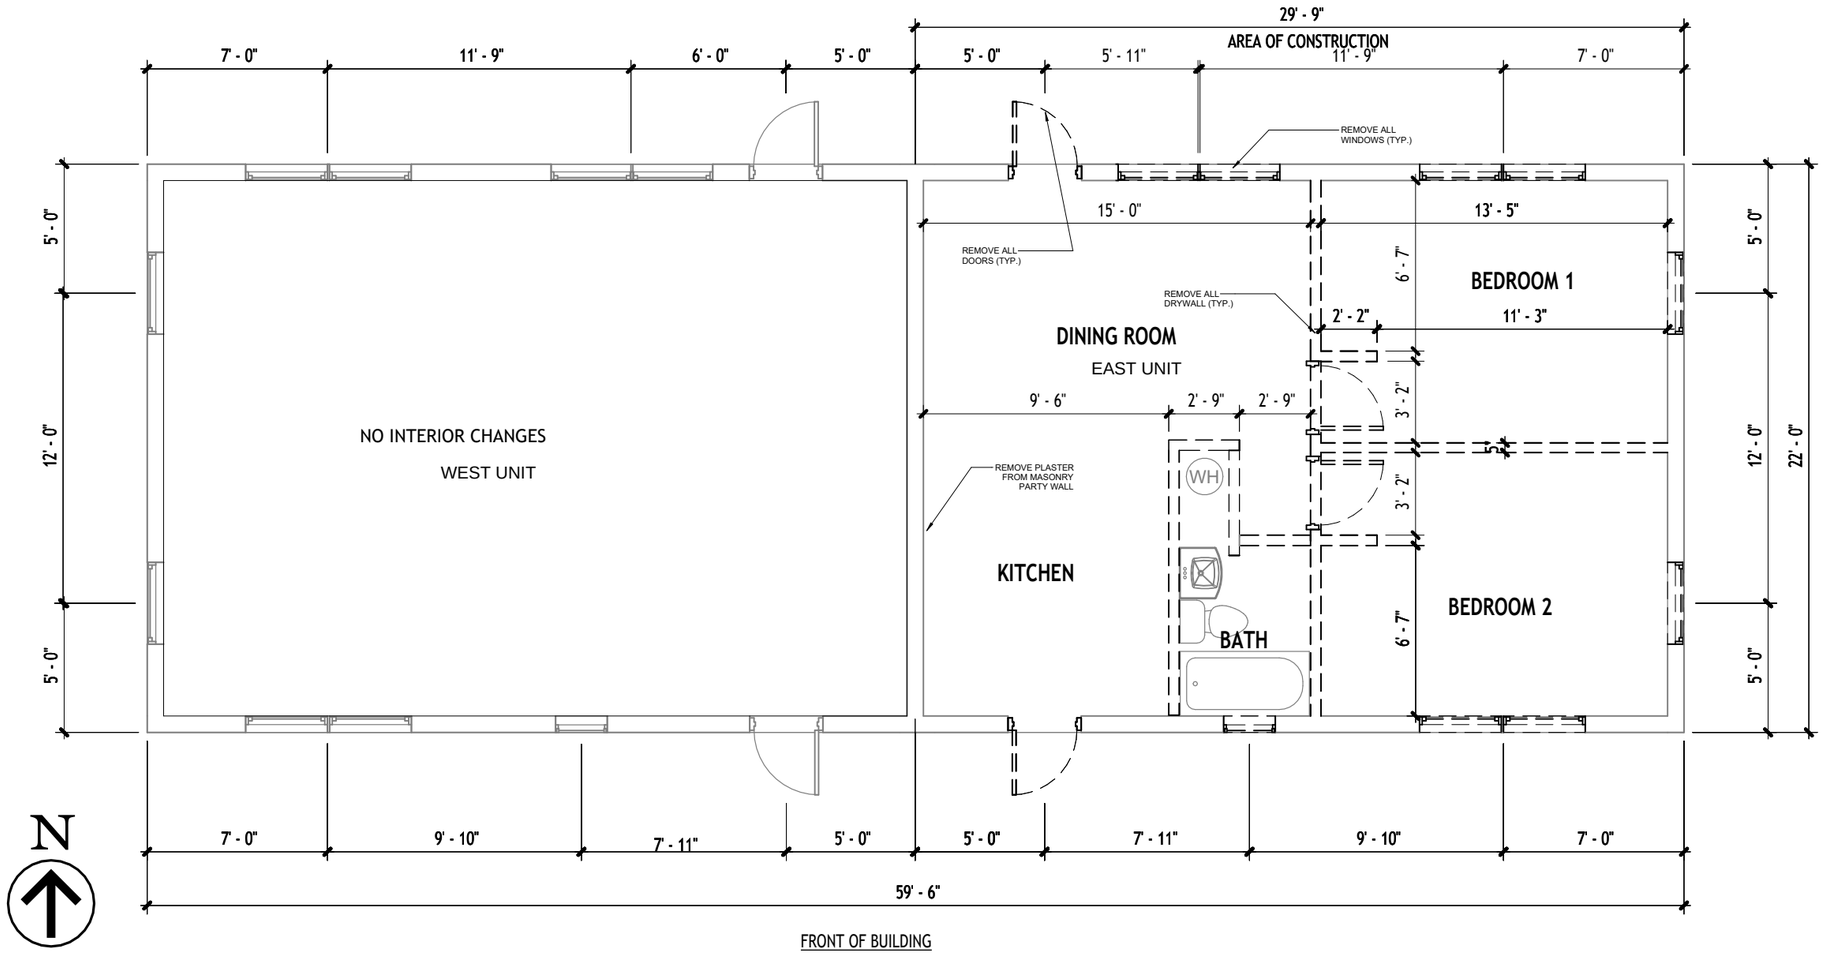

1 Demolition Floor Plan
3/16" = 1'-0"

LEGEND
– TO BE REMOVED

ALL DIMENSIONS ARE FOR REFERENCE PURPOSES ONLY

WWW.RANSOMSOLUTION.COM

CONFIDENTIAL CLIENT

SOUTH FLORIDA, FL
PORTFOLIO SAMPLE - CLIENT INFORMATION REMOVED

FIRE DAMAGE REPAIR

No.	Description	Date

Demolition Floor Plans


Project number	RS-1053
Date	09/04/26
Drawn by	S.B.R.
Checked by	

S102


Scale 3/16" = 1'-0"

SEAL REMOVED
PORTFOLIO SAMPLE

ENGINEER SEAL

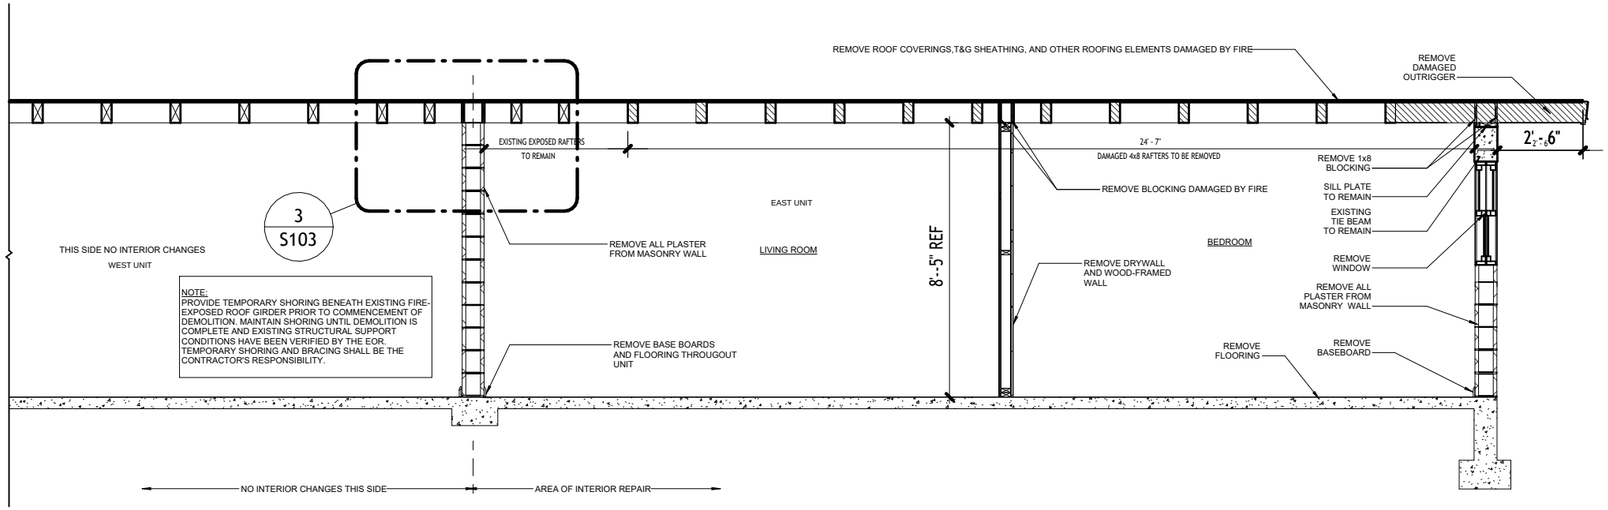


1 E/W Section (E)
1/4" = 1'-0"

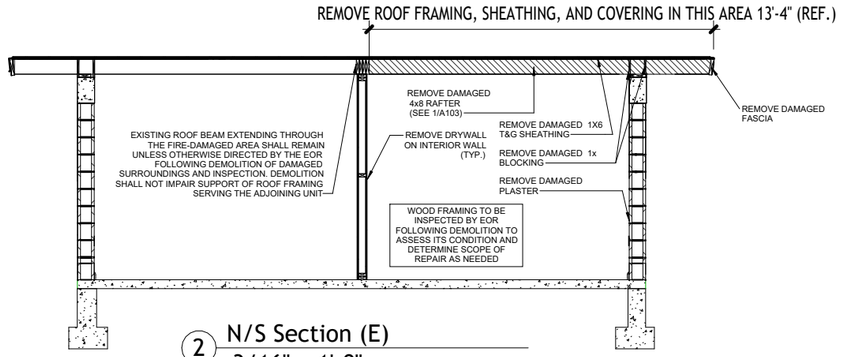

2 N/S Section (E)
3/16" = 1'-0"

NOTE:
PROVIDE TEMPORARY SHORING BENEATH EXISTING FIRE-EXPOSED ROOF GIRDER PRIOR TO COMMENCEMENT OF DEMOLITION. MAINTAIN SHORING UNTIL DEMOLITION IS COMPLETE AND EXISTING STRUCTURAL SUPPORT CONDITIONS HAVE BEEN VERIFIED BY THE EOR. TEMPORARY SHORING AND BRACING SHALL BE THE CONTRACTOR'S RESPONSIBILITY.

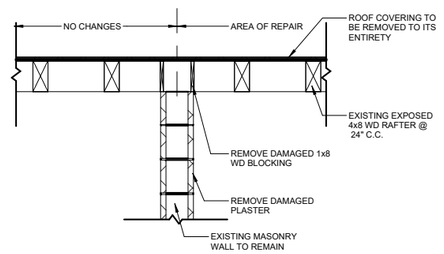

3 Demising Wall - (E)-Detail
3/8" = 1'-0"

NOTE:
EXISTING DEMISING WALL AND ROOF INTERSECTION SHALL BE RECONSTRUCTED TO PROVIDE A CONTINUOUS FIRE-RESISTANCE-RATED SEPARATION BETWEEN DWELLING UNITS. FIRE-RESISTANCE CONTINUITY SHALL BE MAINTAINED AT ALL FRAMING MEMBERS, PENETRATIONS, JOINTS, AND INTERSECTIONS AFFECTED BY THE FIRE DAMAGE AND DEMOLITION WORK .

WWW.RANSOMSOLUTION.COM

CONFIDENTIAL CLIENT

SOUTH FLORIDA, FL

PORTFOLIO SAMPLE - CLIENT INFORMATION REMOVED

FIRE DAMAGE REPAIR

No.	Description	Date

Demolition Sections & Details


Project number	RS-1053
Date	09/04/26
Drawn by	S.B.R.
Checked by	

S103

Scale As indicated

SEAL REMOVED
PORTFOLIO SAMPLE

ENGINEER SEAL

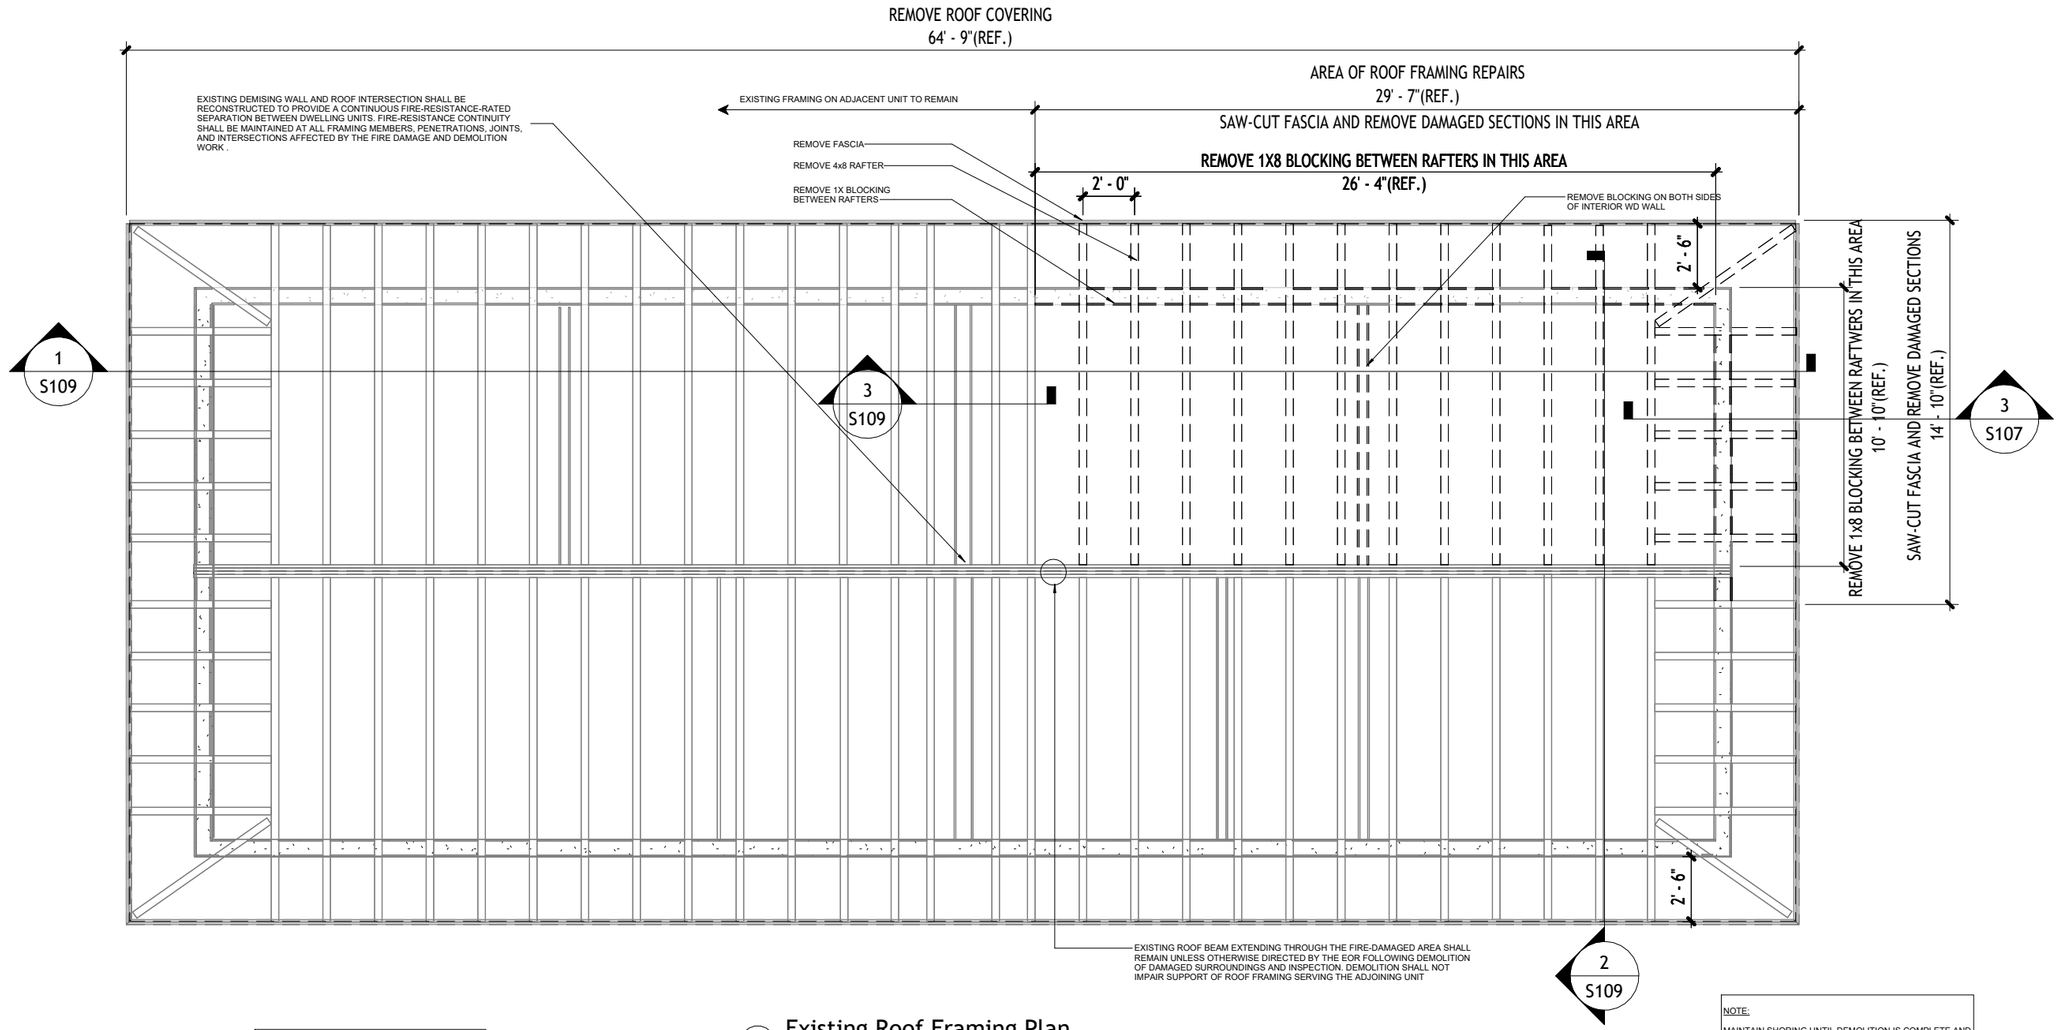

WOOD FRAMING TO BE INSPECTED BY EOR FOLLOWING DEMOLITION TO ASSESS ITS CONDITION AND DETERMINE SCOPE OF REPAIR AS NEEDED

1 Existing Roof Framing Plan
3/16" = 1'-0"

NOTE:

MAINTAIN SHORING UNTIL DEMOLITION IS COMPLETE AND EXISTING STRUCTURAL SUPPORT CONDITIONS HAVE BEEN VERIFIED BY THE EOR. TEMPORARY SHORING AND BRACING SHALL BE THE CONTRACTOR'S RESPONSIBILITY.

LEGEND

- - - - TO BE REMOVED

ALL DIMENSIONS ARE FOR REFERENCE PURPOSES ONLY

WWW.RANSOMSOLUTION.COM

CONFIDENTIAL CLIENT

SOUTH FLORIDA, FL

PORTFOLIO SAMPLE - CLIENT INFORMATION REMOVED

FIRE DAMAGE REPAIR

No.	Description	Date


Existing Roof Framing Plan -Demolition

Project number	RS-1053
Date	09/04/26
Drawn by	S.B.R.
Checked by	
Scale	3/16" = 1'-0"


S104

SEAL REMOVED
PORTFOLIO SAMPLE


ENGINEER SEAL

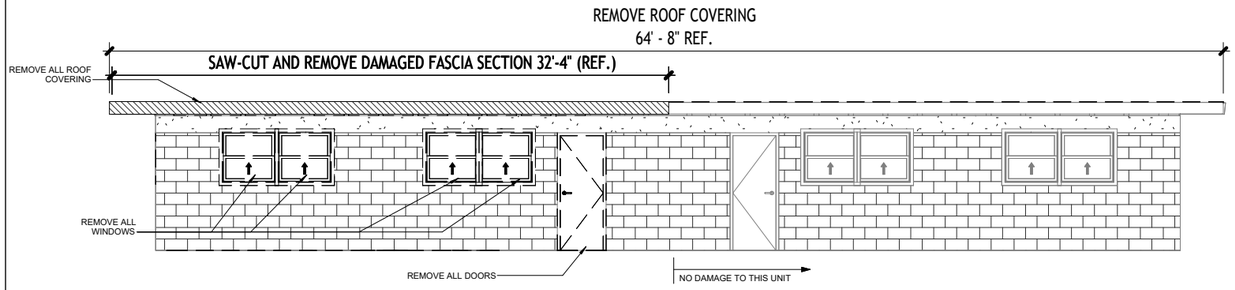


1 North Elevation
1/8" = 1'-0"

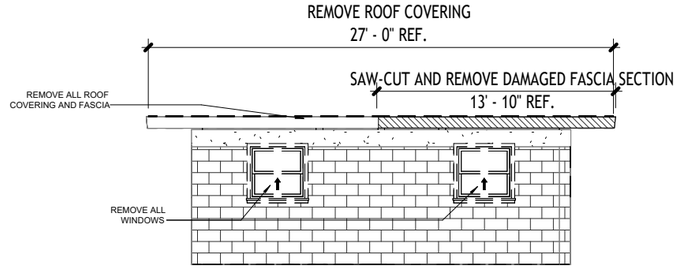

3 East Elevation
1/8" = 1'-0"

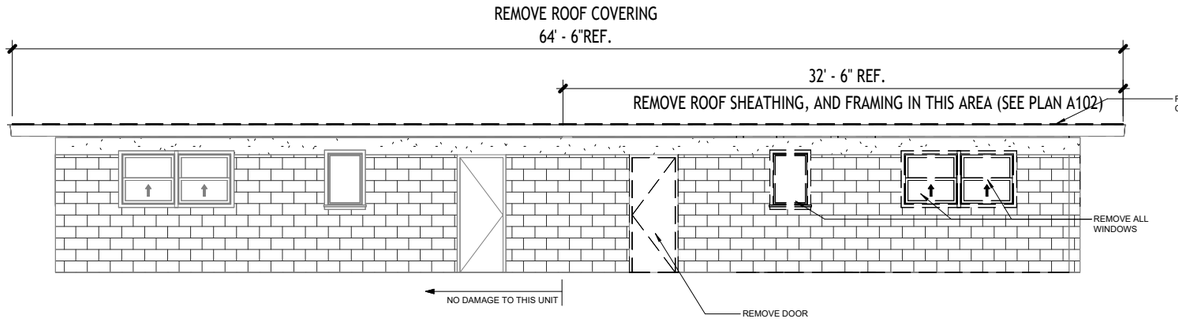

2 South Elevation
1/8" = 1'-0"

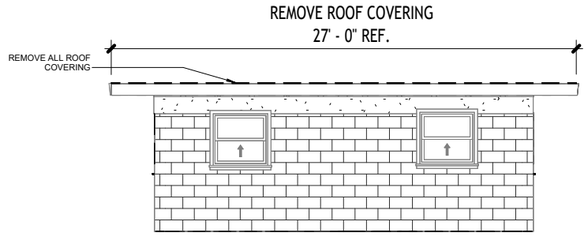

4 West Elevation
1/8" = 1'-0"

ALL DIMENSIONS ARE FOR REFERENCE PURPOSES ONLY

WWW.RANSOMSOLUTION.COM

CONFIDENTIAL CLIENT

SOUTH FLORIDA, FL

PORTFOLIO SAMPLE - CLIENT INFORMATION REMOVED

FIRE DAMAGE REPAIR

No.	Description	Date


Demolition Elevations

Project number	RS-1053
Date	09/04/26
Drawn by	S.B.R.
Checked by	
Scale	1/8" = 1'-0"

S105

SEAL REMOVED
PORTFOLIO SAMPLE

ENGINEER SEAL

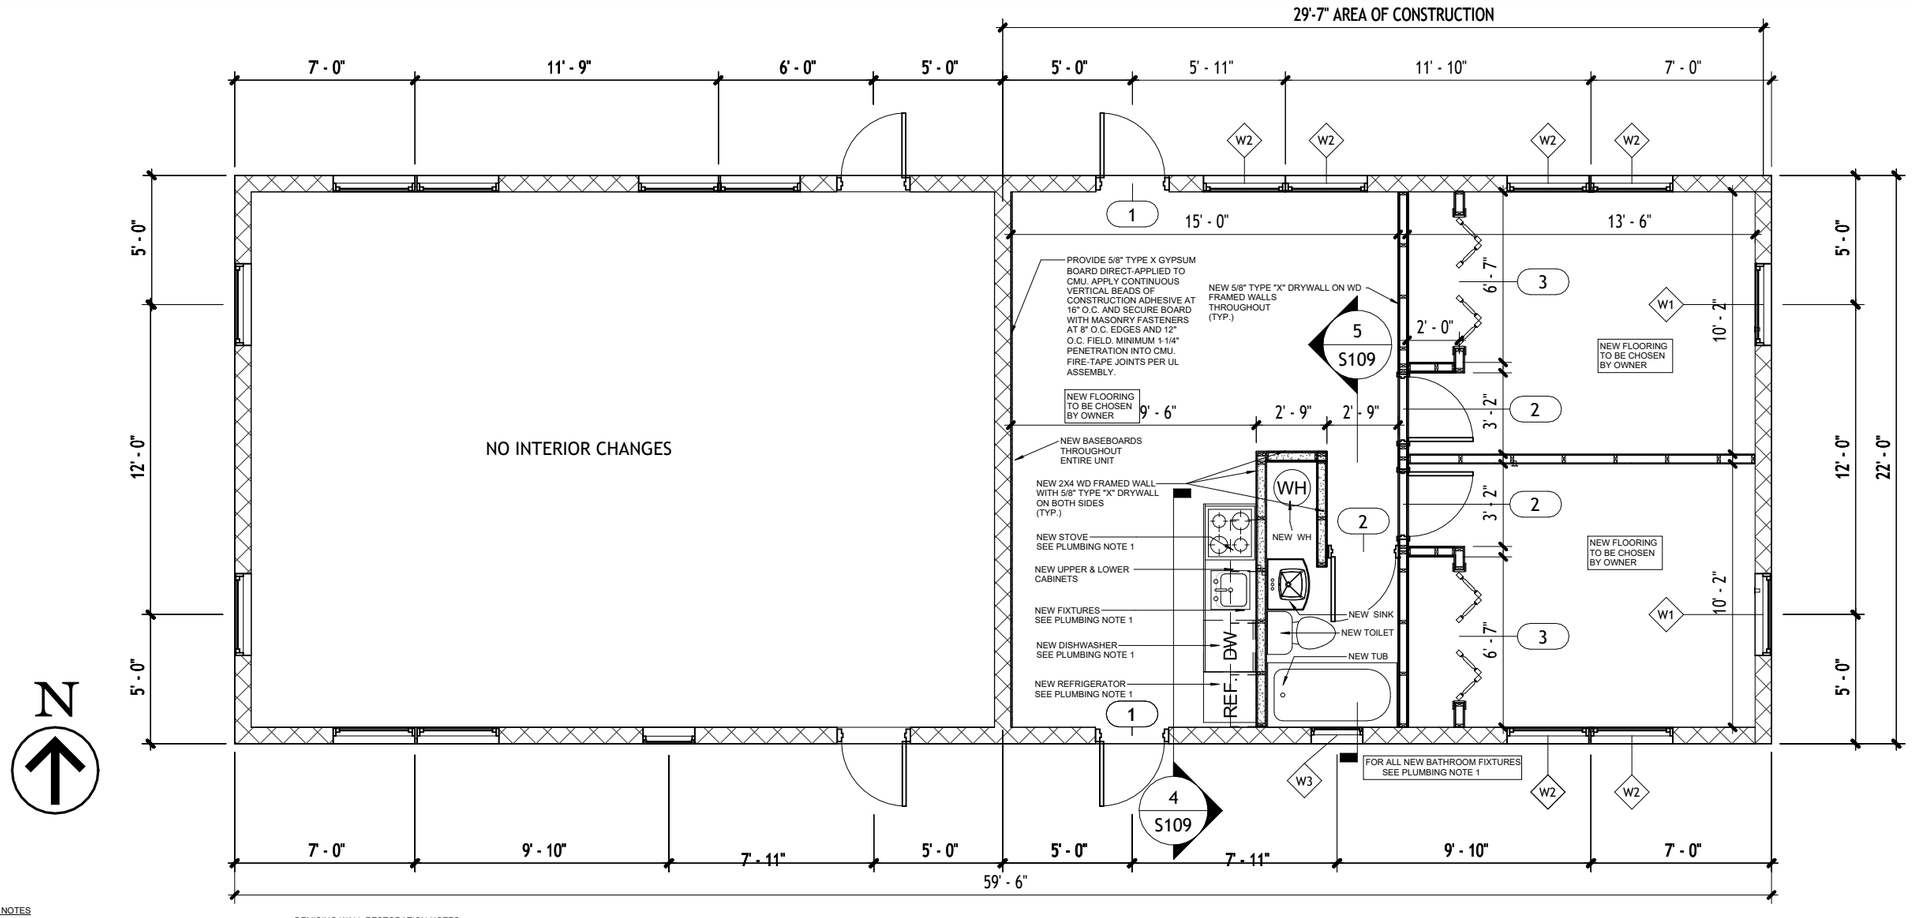

STRUCTURAL REPAIR NOTES

1. FOLLOWING DEMOLITION, EXPOSE ALL SIDES OF EXISTING ROOF BEAMS, RAFTERS, LEDGERS, AND BEARING LOCATIONS FOR EXAMINATION.
2. EXISTING WOOD FRAMING EXHIBITING CHARRING, SPLITTING, SECTION LOSS, EXCESSIVE DEFLECTION, OR DETERIORATION SHALL BE REMOVED AND REPLACED WITH NEW FRAMING MATCHING THE EXISTING MEMBER SIZE UOA BY THE EOR.
3. IF LESS THAN 25% SECTION LOSS ON 4x8 BEAM FOLLOWING CHAR/SOOT REMOVAL, PROVIDE (2) NEW 2X8 SYP NO. 2 MINIMUM SISTER MEMBERS, ONE EACH SIDE OF EXISTING 4X8 BEAM, EXTENDING CONTINUOUSLY OVER THE AFFECTED SPAN AND BEARING DIRECTLY ON EXISTING SUPPORTS. PROVIDE FULL-DEPTH, TIGHT-FITTING CONTACT BETWEEN EXISTING AND NEW MEMBERS. CONNECT NEW SISTER MEMBERS TO EXISTING BEAM WITH 1/2" DIA. THROUGH-BOLTS WITH WASHERS, STAGGERED AT 16" O.C. MAXIMUM. MAINTAIN REQUIRED NDS MINIMUM END AND EDGE DISTANCES. PROVIDE MINIMUM 5-1/2" BEARING AT MASONRY SUPPORT, WHERE AVAILABLE, AND FULL BEARING AT FRAMED SUPPORTS. REMOVE ANY LOOSE, CHARRED, OR STRUCTURALLY UNSOUND WOOD PRIOR TO INSTALLATION. FIELD VERIFY EXISTING BEAM CONDITION AND SUPPORT/BEARING CONDITIONS PRIOR TO COMMENCING WORK.
4. PROVIDE FRAMING ANCHORS, CLIPS, STRAPS, AND FASTENERS AS REQUIRED TO RESTORE LOAD PATH CONTINUITY.
5. REMOVE AND REPLACE FIRE/SMOKE-DAMAGED GYPSUM BOARD WITH NEW 5/8" TYPE "X" GYPSUM BOARD AT PARTITION WALL BETWEEN BEDROOM AND LIVING AREA. FINISH IN ACCORDANCE TO MANUFACTURER'S SPECIFICATIONS. MATCH EXISTING WALL CONSTRUCTION AND FINISHES.

DEMISING WALL RESTORATION NOTES

1. RESTORE THE EXISTING SEPARATION BETWEEN DWELLING UNITS AT ALL LOCATIONS AFFECTED BY THE DEMOLITION AND FIRE DAMAGE.
2. REMOVE ALL LOOSE, DAMAGED, DETERIORATED PLASTER, MORTAR, SEALANTS, FIREBLOCKING MATERIALS, AND FINISHES AT THE TOP OF THE DEMISING WALL.
3. FILL ALL CONCEALED OPENINGS AND VOIDS BETWEEN THE TOP OF THE CMU/TIE BEAM WALL AND ADJACENT WOOD FRAMING WITH MINERAL WOOL FIRE SAFING.
4. PROVIDE CONTINUOUS FIREBLOCKING ALONG THE ENTIRE LENGTH OF THE DEMISING WALL WHERE EXPOSED DURING DEMOLITION.
5. SEAL EXPOSED JOINTS BETWEEN MASONRY WOOD FRAMING, AND FIRE SAFING MATERIALS WITH APPROVED FIRE-RESISTANT SEALANT.
6. RESTORE WALL FINISHES TO MATCH ADJACENT EXISTING CONSTRUCTION.
7. CONTRACTOR SHALL NOTIFY EOR IF DEMOLITION REVEALS CONDITIONS SUBSTANTIALLY DIFFERENT FROM THOSE ANTICIPATED BY THESE DRAWINGS.

PLUMBING NOTES

1. PLUMBING SCOPE UNDER THIS PERMIT IS LIMITED TO LIKE-FOR-LIKE REPLACEMENT OF THE FIXTURES SHOWN HEREON (SINK, TOILET, TUB, WATER HEATER, DISHWASHER). EXISTING SUPPLY, DWV PIPING, VENTS, AND ROUGH-IN LOCATIONS ARE NOT BEING RELOCATED, RESIZED, OR ALTERED. NO PLUMBING PLAN SHEETS ARE REQUIRED FOR THIS SCOPE.
2. NEW FIXTURES SHALL CONNECT TO EXISTING SUPPLY AND DRAIN ROUGH-INS AT THEIR CURRENT LOCATIONS. WHERE A NEW FIXTURE'S CONNECTION POINTS DIFFER FROM THE UNIT BEING REMOVED, CONTRACTOR SHALL FIELD-VERIFY AND ADAPT USING STANDARD FITTINGS; ANY CONDITION REQUIRING RELOCATION OF ROUGH-IN PIPING IS OUTSIDE THIS SCOPE AND SHALL BE REPORTED TO THE DESIGNER/EOR PRIOR TO PROCEEDING.
3. NEW WATER HEATER SHALL MATCH EXISTING CAPACITY, FUEL TYPE, AND LOCATION. VENTING/COMBUSTION AIR (IF APPLICABLE) AND T&P RELIEF DISCHARGE SHALL COMPLY WITH FBC-PLUMBING AS CURRENTLY INSTALLED. ANY DEVIATION FROM EXISTING VENTING CONFIGURATION REQUIRES SEPARATE REVIEW.
4. NO NEW PLUMBING FIXTURE UNITS ARE ADDED; FIXTURE COUNT AND TYPE MATCH EXISTING. CONTRACTOR SHALL VERIFY NO CONCEALED FIRE, SMOKE, OR WATER DAMAGE EXISTS ON EXPOSED SUPPLY, DRAIN, OR VENT PIPING IN THE REPAIR AREA PRIOR TO FIXTURE SET AND WALL/CEILING CLOSURE; REPORT ANY DAMAGE TO DESIGNER/EOR PRIOR TO CONCEALMENT.

FRONT OF BUILDING

1 Repair Floor Plan
3/16" = 1'-0"

LEGEND

- EXISTING MASONRY WALL
- EXISTING 2x4 WOOD FRAMED WALL WITH NEW 5/8" TYPE "X" GYPSUM WALLBOARD ON BOTH SIDES
- NEW 2x4 WOOD FRAMED WALL WITH NEW 5/8" TYPE "X" GYPSUM WALLBOARD ON BOTH SIDES (KITCHEN & BATHROOM)
- W1 - NEW WINDOW (SEE SCHEDULE A110)
- 1 - NEW DOOR (SEE DOOR SCHEDULE A110)

ALL DIMENSIONS ARE FOR REFERENCE PURPOSES ONLY

WWW.RANSOMSOLUTION.COM

CONFIDENTIAL CLIENT

SOUTH FLORIDA, FL

PORTFOLIO SAMPLE - CLIENT INFORMATION REMOVED

FIRE DAMAGE REPAIR

No.	Description	Date


Repair Floor Plans

Project number	RS-1053
Date	09/04/26
Drawn by	S.B.R.
Checked by	
Scale	3/16" = 1'-0"

S106

SEAL REMOVED
PORTFOLIO SAMPLE

ENGINEER SEAL

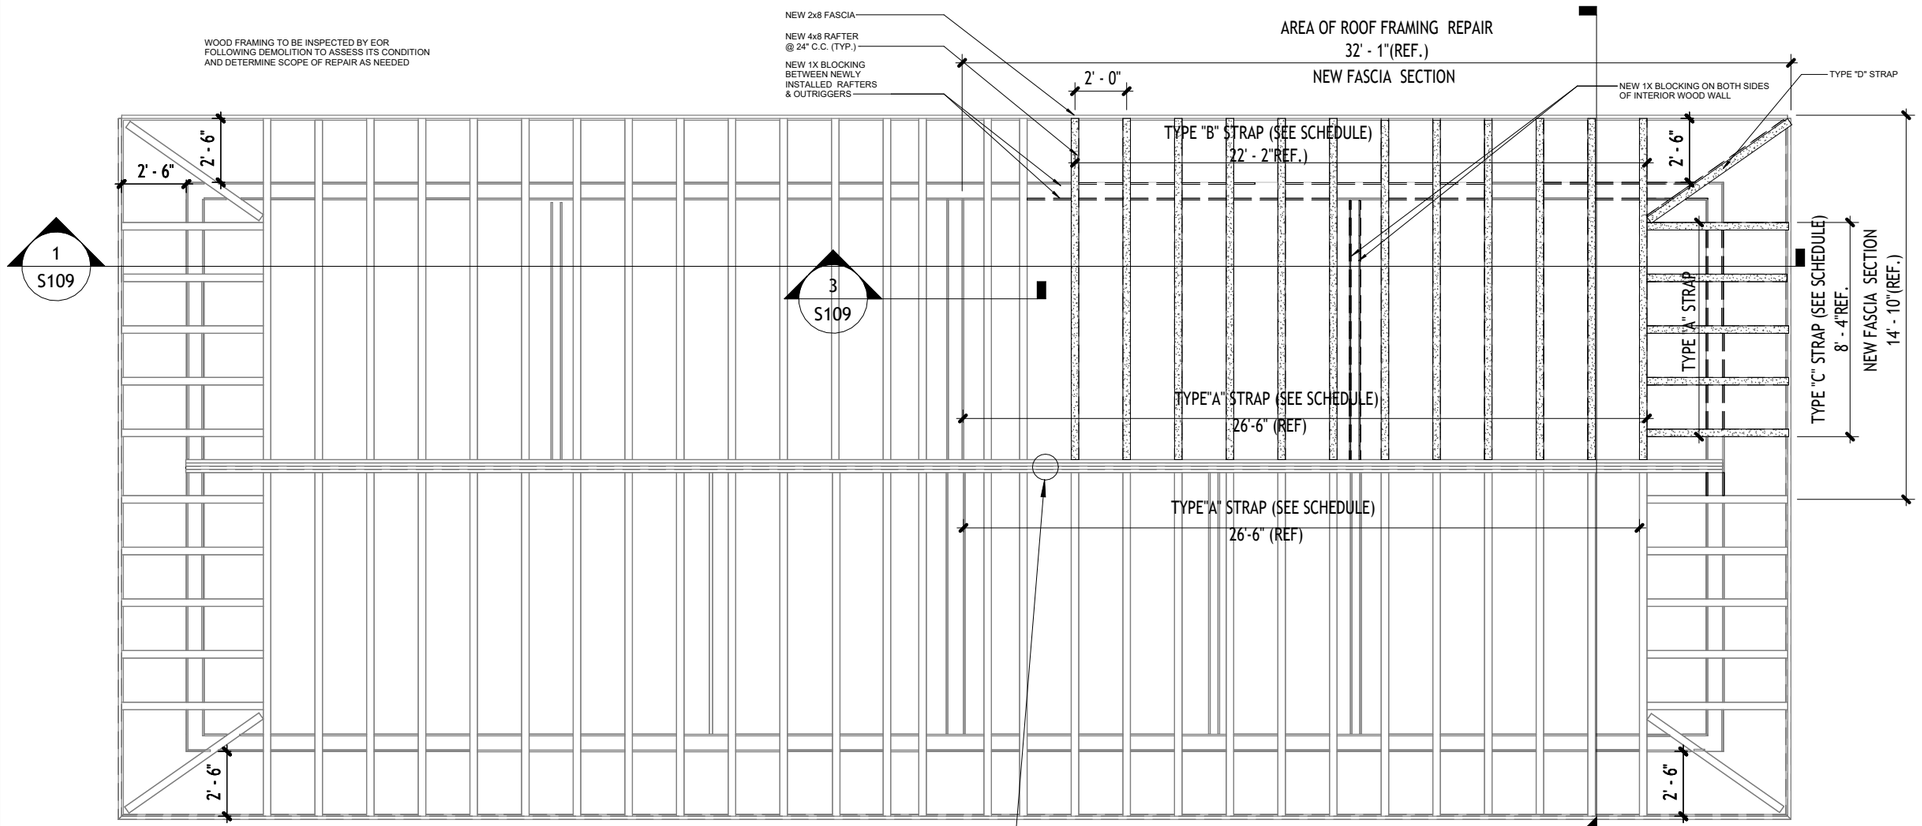

STRAP SCHEDULE - (ALL STRAPS ARE SIMPSON STRONG-TIE)							
DESIGNATION	TYPE	SUPPORTING MEMBER FASTENERS	SUPPORTING MEMBER FASTENERS	APPLICATION	ALLOWABLE UPLIFT LOAD	MAXIMUM UPLIFT LOAD	COMMENTS
"A"	(1) LUS48	16D COMMON NAILS, 0.162" DIA. × 3 1/2" LONG	MAX. (6) 16D COMMON NAILS, 0.162" DIA. × 3 1/2" LONG	4X8 WOOD BM/JOIST TO WD HEADER: STANDARD FLANGE		1,135 LBS	14-GA G90 GALV. FACE-MOUNT HANGER
"B"	(2) HL55	(8) 1/2" DIA. BOLTS	MAX. (6) 10D COMMON NAILS, 0.148" DIA. × 3 1/2" LONG	4X8 WOOD BM/JOIST TO WD HEADER:CONCEALED FLANGE		1,110 LBS	14-GA G90 GALV. CONCEALED-FLANGE HANGER
"C"	(1) LS70	(6) #10 SCREWS	RAFTER: (7) 0.148" DIA X 1 1/2" CONNECTOR NAILS	4X8 WD RAFTER TO CONCRETE TIE BEAM			14-GA. 20 HEAVY TWIST STRAP
"D"	(1) HUC48	(9) 0.148 X 3" NAILS	RAFTER: (7) 0.148" DIA X 1 1/2" CONNECTOR NAILS	4X8 WD RAFTER TO FULLY GROUTED CMU			ANCHOR INTO FULLY GROUTED CELL OR TIE-BEAM ONLY


EXISTING ROOF BEAM EXTENDING THROUGH THE FIRE-DAMAGED AREA SHALL REMAIN UNLESS OTHERWISE DIRECTED BY THE EOR FOLLOWING DEMOLITION OF DAMAGED SURROUNDINGS AND INSPECTION. DEMOLITION SHALL NOT IMPAIR SUPPORT OF ROOF FRAMING SERVING THE ADJOINING UNIT.

IF LESS THAN 25% SECTION LOSS ON 4x8 BEAM FOLLOWING CHAR/SOOT REMOVAL, PROVIDE (2) NEW 2X8 SYP NO. 2 MINIMUM SISTER MEMBERS, ONE EACH SIDE OF EXISTING 4X8 BEAM, EXTENDING CONTINUOUSLY OVER THE AFFECTED SPAN AND BEARING DIRECTLY ON EXISTING SUPPORTS. PROVIDE FULL-DEPTH, TIGHT-FITTING CONTACT BETWEEN EXISTING AND NEW MEMBERS. CONNECT NEW SISTER MEMBERS TO EXISTING BEAM WITH 1/2" DIA. THROUGH-BOLTS WITH WASHERS, STAGGERED AT 16" O.C. MAXIMUM. MAINTAIN REQUIRED NDS MINIMUM END AND EDGE DISTANCES. PROVIDE MINIMUM 5-1/2" BEARING AT MASONRY SUPPORT, WHERE AVAILABLE, AND FULL BEARING AT FRAMED SUPPORTS. REMOVE ANY LOOSE, CHARRED, OR STRUCTURALLY UNSOUND WOOD PRIOR TO INSTALLATION. FIELD VERIFY EXISTING BEAM CONDITION AND SUPPORT/BEARING CONDITIONS PRIOR TO COMMENCING WORK.


LEGEND

- AREAS OF NEW CONSTRUCTION

1 Existing Roof Framing Plan
3/16" = 1'-0"

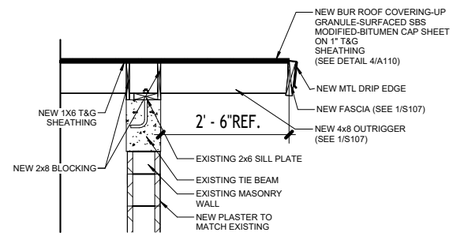

3 Roof Edge Detail - Detail
3/8" = 1'-0"

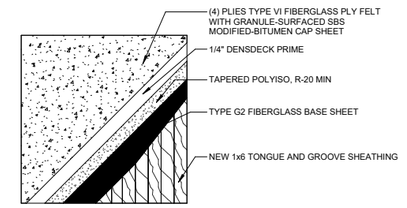

4 ROOF COVERING DETAIL
3/16" = 1'-0"

ALL DIMENSIONS ARE FOR REFERENCE PURPOSES ONLY

INSTALL NEW BUR ROOFING SYSTEM OVER PREPARED SUBSTRATE, INCLUDING ALL REQUIRED FLASHINGS, TERMINATIONS, AND ACCESSORIES, PER MANUFACTURER'S SPECIFICATIONS AND APPLICABLE CODES.

GENERAL FASTENER NOTES

1. PROVIDE SIMPSON STRONG-TIE CONNECTORS OF THE MODEL AND FINISH INDICATED. INSTALL CONNECTORS AND FASTENERS IN STRICT ACCORDANCE WITH THE CURRENT MANUFACTURER'S PUBLISHED INSTALLATION INSTRUCTIONS, APPLICABLE EVALUATION REPORTS, AND STRUCTURAL ENGINEERS DESIGN.

2. FASTENER QUANTITIES, DIAMETERS, LENGTHS, TYPES AND LOCATIONS SHALL MATCH THE CONNECTOR SCHEDULE. INSTALL ALL FASTENERS REQUIRED FOR THE SCHEDULED CONNECTION CAPACITY. UNUSED OPTIONAL HOLES ARE PERMITTED ONLY WHERE THE ENGINEER'S DESIGN IS BASED ON THE PUBLISHED MINIMUM FASTENING PATTERN.

3. DO NOT SUBSTITUTE ROOFING NAILS, BOX NAILS, FINISH NAILS, DRYWALL SCREWS, DECK SCREWS OR GENERIC STRUCTURAL SCREWS FOR THE SPECIFIED CONNECTOR FASTENERS. SIMPSON STRONG-DRIVE SD CONNECTOR SCREWS MAY BE USED ONLY WHERE THE EXACT CONNECTOR AND SCREW SUBSTITUTION ARE EXPRESSLY LISTED BY SIMPSON STRONG-TIE OR APPROVED BY THE ENGINEER. Simpson emphasizes that connector capacity depends on installing the specified fastener type, size, quantity and hole location.

4. FASTENER AND CONNECTOR COATINGS SHALL BE COMPATIBLE WITH EACH OTHER, THE WOOD PRESERVATIVE TREATMENT AND THE SERVICE ENVIRONMENT. PROVIDE HOT-DIP GALVANIZED, ZMAX OR STAINLESS-STEEL CONNECTORS AND MATCHING FASTENERS WHERE REQUIRED FOR EXTERIOR, WET, COASTAL OR PRESERVATIVE-TREATED-WOOD CONDITIONS.

5. SEAT EACH WOOD MEMBER FULLY AND TIGHTLY IN THE HANGER. DO NOT MODIFY, CUT, WELD, DRILL OR REPEATEDLY FIELD-BEND CONNECTORS. HTSM20 STRAPS MAY BE FIELD-BENT ONCE UP TO 45 DEGREES WHERE PERMITTED BY THE MANUFACTURER.

6. THE STRUCTURAL ENGINEER SHALL VERIFY CONNECTOR CAPACITY, WOOD SPECIES AND GRADE, SUPPORTING-MEMBER THICKNESS, END AND EDGE DISTANCES, MASONRY GROUTING, CONCRETE STRENGTH, ANCHOR EMBEDMENT, WIND UPLIFT AND GRAVITY REACTIONS BEFORE CONSTRUCTION.

WWW.RANSOMSOLUTION.COM

CONFIDENTIAL CLIENT

SOUTH FLORIDA, FL

PORTFOLIO SAMPLE - CLIENT INFORMATION REMOVED

FIRE DAMAGE REPAIR

No.	Description	Date

Repair Roof Plan


Project number	RS-1053
Date	09/04/26
Drawn by	S.B.R.
Checked by	

S107


Scale As indicated

SEAL REMOVED
PORTFOLIO SAMPLE


ENGINEER SEAL

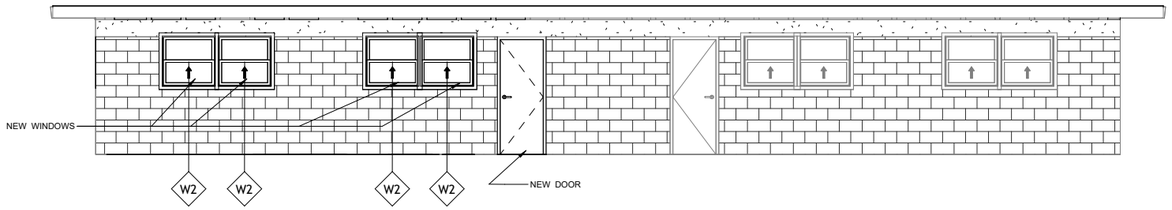


1 North Elevation
1/8" = 1'-0"

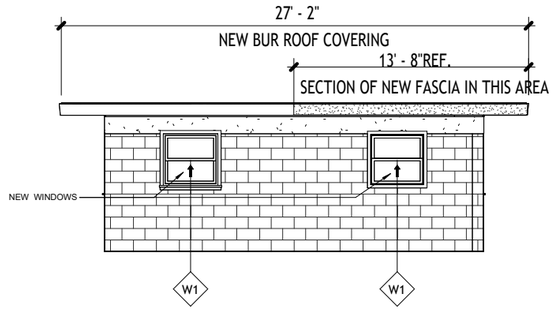

2 East Elevation
1/8" = 1'-0"

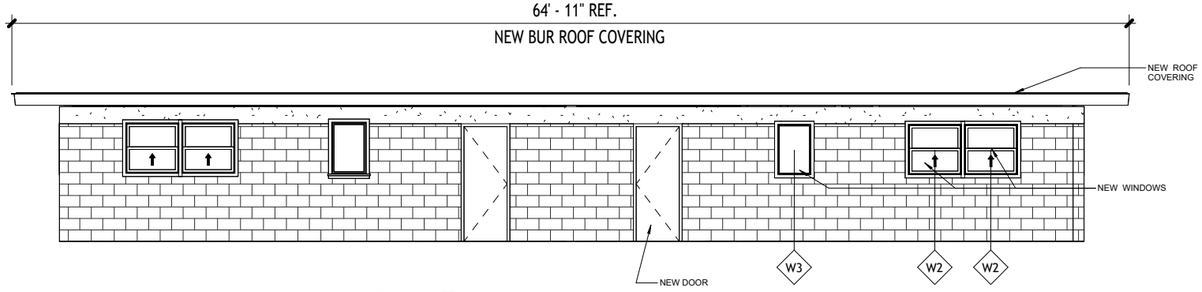

3 South Elevation
1/8" = 1'-0"

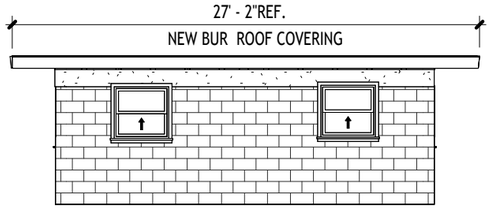

4 West Elevation
1/8" = 1'-0"

ALL DIMENSIONS ARE FOR REFERENCE PURPOSES ONLY

WWW.RANSOMSOLUTION.COM

CONFIDENTIAL CLIENT

SOUTH FLORIDA, FL

PORTFOLIO SAMPLE - CLIENT INFORMATION REMOVED

FIRE DAMAGE REPAIR

No.	Description	Date

Repair Elevations


Project number	RS-1053
Date	09/04/26
Drawn by	S.B.R.
Checked by	

S108


Scale 1/8" = 1'-0"

SEAL REMOVED
PORTFOLIO SAMPLE


ENGINEER SEAL

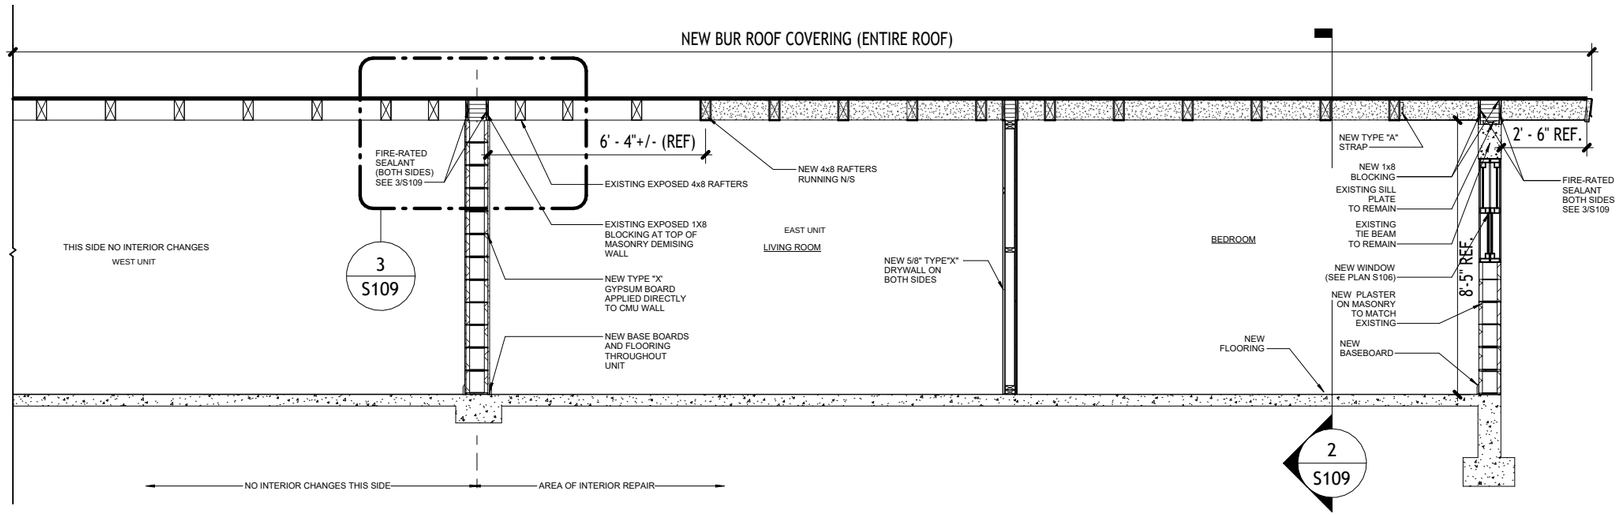


1 E/W Section -Repair
1/4" = 1'-0"

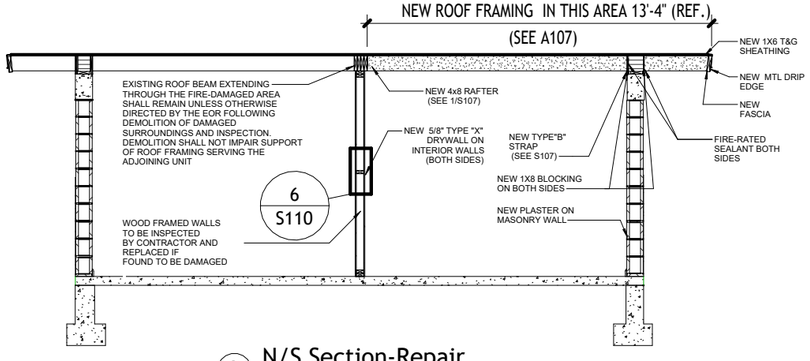


2 N/S Section-Repair
3/16" = 1'-0"

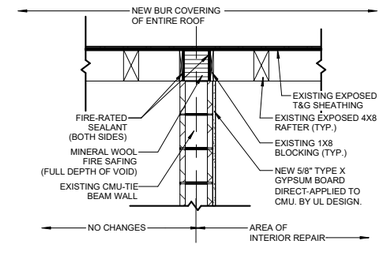

3 Demising Wall Detail-Repair
3/8" = 1'-0"

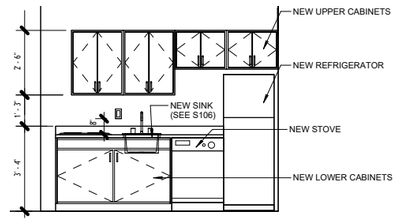

4 Kitchen Elevation
3/16" = 1'-0"

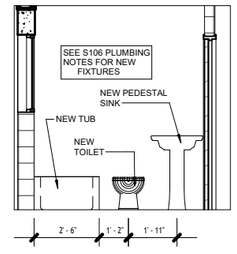

5 Bathroom Elevation
3/16" = 1'-0"

ALL DIMENSIONS ARE FOR REFERENCE PURPOSES ONLY

WWW.RANSOMSOLUTION.COM

CONFIDENTIAL CLIENT

SOUTH FLORIDA, FL

PORTFOLIO SAMPLE - CLIENT INFORMATION REMOVED

FIRE DAMAGE REPAIR

No.	Description	Date

Repair Sections & Details


Project number	RS-1053
Date	09/04/26
Drawn by	S.B.R.
Checked by	

S109

Scale As indicated


SEAL REMOVED
PORTFOLIO SAMPLE

ENGINEER SEAL

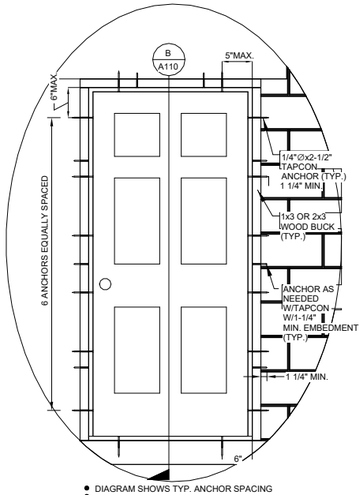


- DIAGRAM SHOWS TYP. ANCHOR SPACING
- 3/16 ∅ TAPCON ANCHOR INSTALLED THROUGH FRAME AND BUCK INTO CONCRETE/MASONRY MINIMUM EMBEDMENT INTO CONCRETE/MASONRY SHALL BE 1 1/4"

A - DOOR ELEVATION

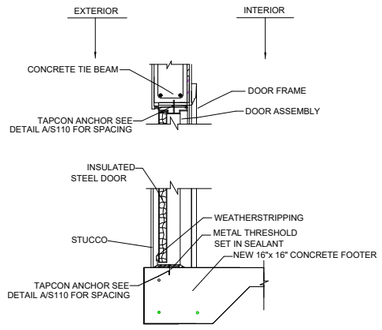


B - DOOR SECTION

1 DOOR DETAIL
3/8" = 1'-0"

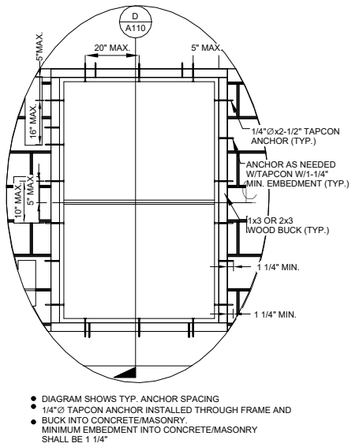


- DIAGRAM SHOWS TYP. ANCHOR SPACING
- 1/4"∅ TAPCON ANCHOR INSTALLED THROUGH FRAME AND BUCK INTO CONCRETE/MASONRY. MINIMUM EMBEDMENT INTO CONCRETE/MASONRY SHALL BE 1 1/4"

C - WINDOW ELEVATION

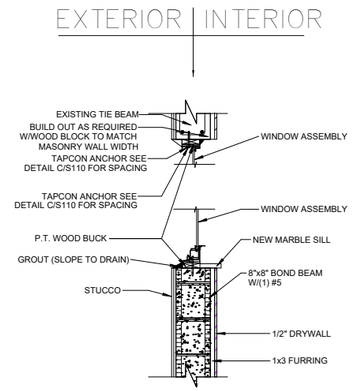

D - WINDOW SECTION


2 TYP. WINDOW DETAIL
3/8" = 1'-0"

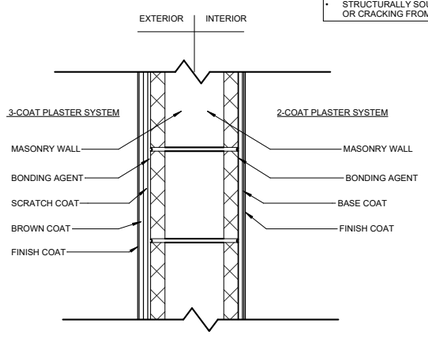

FIRE-DAMAGED MASONRY MUST BE:

- SCRAPED AND CLEANED OF SOOT, CHAR, AND LOOSE MATERIAL
- MOISTURE-CHECKED
- STRUCTURALLY SOUND (NO SPALLING OR CRACKING FROM HEAT)

3 Ext. Masonry Wall Details
1" = 1'-0"

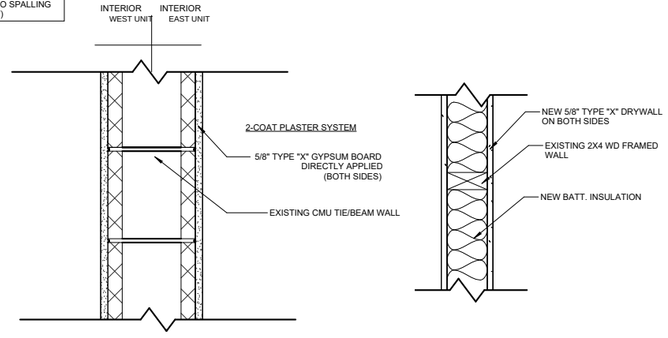

6 Typ. Interior Wall Detail
1" = 1'-0"

Door Schedule

Mark	Type	Product Rated Pressure	Required Design Pressue	Rough W X H	Door W X H	Zone	FL Product Approval	IMPACT RESISTANCE
1	30" x 80" MASONITE BUILDER SERIES SIX PANEL- OUTSWING SGL DOOR	+/- 70.0 PSF	+21.79 PSF/-23.69 PSF	32" X 82	30" X 80"	4	FL22513.6-R5	YES
2	30" x 80" MASONITE BUILDER SERIES SIX PANEL- HOLLOW INTERIOR DOOR			32" X 82	30" X 80"			
3	BIIFOLD WOOD DOOR			62 x 82"	60" X 80"			

Window Schedule

Type Mark	Operation	Existing Opening	Config./Mullion	Mfr.	FL APPROVAL	REQ'D DP	PRODUCT DP	ZONE
W1	CASEMENT	36" x38 1/2"	SINGLE W-1 UNIT-EGRESS	CUSTOM WINDOW SYSTEMS INC.	FL6890-R8	+22.8/-30.4 PSF	+/- 67.5 PSF	5
W2	SINGLE-HUNG	36" x77 1/2"	SH-8100 CONT. H.D. & SILL (DBL SINGLE HUNG, iMPACT)	CUSTOM WINDOW SYSTEMS INC.	FL5823-R13	+21.79 / -23.69 PSF/+21.79 / -28.38 PSF	+/- 67.5 PSF	4/5
W3	SINGLE-HUNG	24" x36"	SINGLE UNIT	CUSTOM WINDOW SYSTEMS INC.	FL5823-R13	+22.8/-24.7 PSF	+/- 67.5 PSF	4

WWW.RANSOMSOLUTION.COM

CONFIDENTIAL CLIENT

SOUTH FLORIDA, FL

PORTFOLIO SAMPLE - CLIENT INFORMATION REMOVED

FIRE DAMAGE REPAIR

No.	Description	Date

Window & Detail Sections

Project number	RS-1053
Date	09/04/26
Drawn by	S.B.R.
Checked by	


S110

Scale As indicated

SEAL REMOVED

PORTFOLIO SAMPLE

ENGINEER SEAL

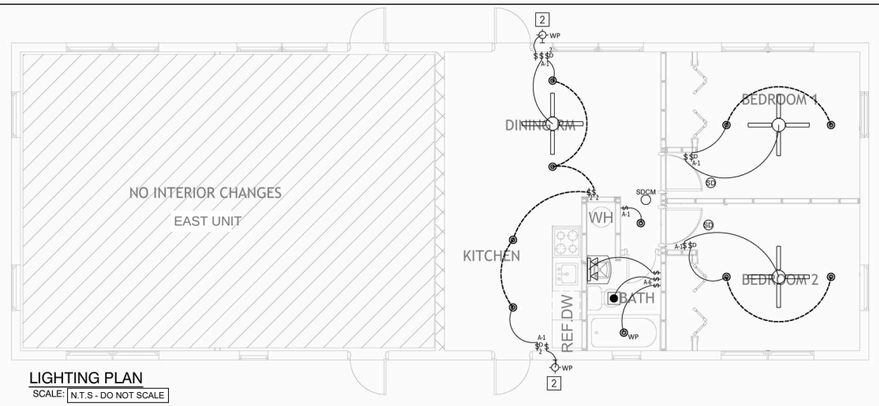

LIGHTING PLAN

SCALE: N.T.S - DO NOT SCALE

LEGEND - LIGHTING FIXTURE

- RECESSED CAN
- EXTERIOR WALL SCONCE
- FAN WITH LIGHT
- VANITY LIGHT
- CEILING FAN

NEW WORK GENERAL NOTES:


1. REFER TO COVER SHEET DRAWING FOR ELECTRICAL LEGENDS & ADDITIONAL INFORMATION
2. COORDINATE WITH ARCHITECT FOR EXACT LOCATION OF ALL ELECTRICAL DEVICES SUCH AS SWITCHES, POWER/TELE/DATA OUTLETS, EQUIPMENT, ETC. PRIOR INSTALLATION.
3. CIRCUIT NUMBERS INDICATED ON BRANCH CIRCUIT HOMERUNS ARE FOR DESIGN PURPOSES ONLY. CONTRACTOR SHALL COORDINATE ACTUAL CIRCUIT NUMBERS AT THE TIME OF INSTALLATION AND SHALL PROVIDE AN ACCURATE, TYPED PANEL ABOARD DIRECTORY FOR EACH PANELBOARD. ANY UNUSED BREAKER SHALL AE TURNED TO THE "OFF" POSITION, AND LABELED AS SPARE.

NEW WORK LIGHTING NOTES:

1. CONTRACTOR SHALL CONNECT TO DESIGNATED PANEL RUN 2#12+1#12G . CONTRACTOR SHALL CONNECT NO MORE THAN 1800 WATTS PER 1-1P-20A-120V C/A.
2. ALL EXTERIOR LIGHTING FIXTURES TO BE CONTROLLED DUSK & DAWN PHOTOCELL ELECTRIC SENSOR. WIRE ACCORDINGLY TO HOUSE PANEL. USE WIRE #12. LOCATE PHOTO ELECTRIC CONTROL AS NECESSARY FOR PROPER FUNCTION OF LIGHTING.

NOTE:

BATHROOMS CONTAINING A BATHTUB, SHOWER, OR TUB/SHOWER SHALL BE MECHANICALLY VENTED FOR HUMIDITY CONTROL

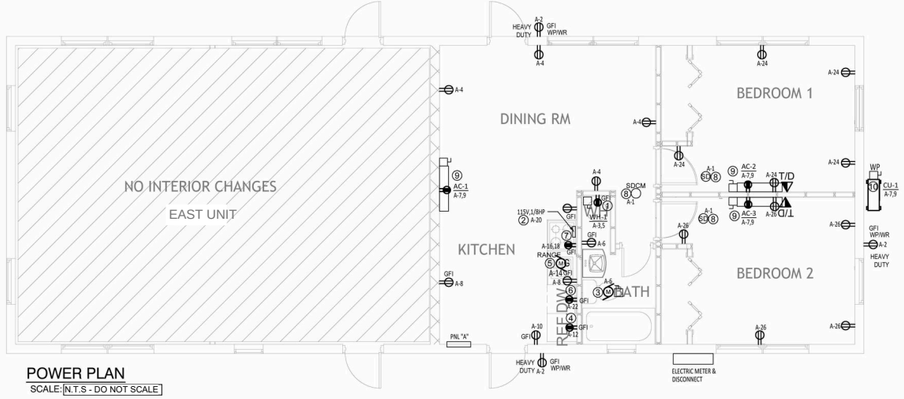

POWER PLAN

SCALE: N.T.S - DO NOT SCALE

LEGEND - ELECTRICAL

- DUPLEX OUTLET
- DEDICATED OUTLET
- GARBAGE DISPOSAL
- SMOKE DETECTOR
- SDCM — SMOKE DETECTOR/ CARBON MONOXIDE DETECTOR COMBO
- T/D — TELE/DATA OUTLET

NEW WORK POWER NOTES: P

1. PROVIDE CONNECTION FOR WATER HEATER (WH-1) PROVIDE DISC. SW. PER NEC REQUIREMENTS. ALL EQUIPMENT TO BE ENERGY STAR.
2. PROVIDE CONNECTION FOR KITCHEN DUCTED HOOD FAN, PROVIDE MEANS OF DISC. TO COMPLY WITH NEC REQUIREMENTS. FAN TO BE CONTROLLED VIA WALL-MOUNTED SWITCH FURNISHED AY HVAC CONTRACTOR. HOOD TO BE ENERGY STAR.
3. PROVIDE CONNECTION FOR BATHROOM EXHAUST FAN, PROVIDE MEANS OF DISC. TO COMPLY WITH NEC REQUIREMENTS. EXHAUST FAN TO BE ENERGY STAR.
4. PROVIDE DED. RECEPTACLE FOR FULL HEIGHT REFRIGERATOR 120V-1PH. PROVIDE GFCI CIRCUIT BREAKER. REFRIGERATOR TO BE ENERGY STAR.
5. CONNECTION FOR GARBAGE DISPOSER WITH NEUMATIC SWITCH IN COUNTER. FHP-120V-1 PHASE PROVIDE MEANS OF DISCONNECT TO COMPLY WITH NEC REQUIREMENTS.
6. PROVIDE DED. GFI RECEPTACLE FOR DISHWASHER. COORDINATE EXACT LOCATION AND HEIGHT PRIOR TO ROUGH-IN. DISHWASHER TO BE ENERGY STAR.
7. PROVIDE CONNECTION FOR RANGE. COORDINATE WITH OWNER FOR REQUIREMENTS
8. WIRE UNIT SMOKE DETECTORS/CO SENSOR SUCH THAT ACTUATION OF ONE ALARM WILL ACTIVATE ALL OF THE ALARMS IN THE INDIVIDUAL UNIT. PROVIDE HARDWIRE COMBINATION UNIT SMOKE DETECTOR/ CO SENSOR WITH BATTERY BACKUP. DEVICE SHALL AE LOCATED 3 FEET AWAY FROM HVAC DIFFUSER AND BATHROOM OR KITCHEN ENTRANCE.
9. PROVIDE CONNECTION FOR INDOOR UNIT, 115V, 1PH, 3W. PROVIDE DISCONNECT SWITCH PER NEC REQUIREMENTS.
10. PROVIDE CONNECTION FOR OUTDOOR UNIT. CU-1 , 230-208V, 1PH. PROVIDE NEMA TYPE 3R 1-208V WP DISC. SW. (UL CLASS RK5). ALL EQUIPMENT PROVIDED TO BE ENERGY STAR RATED.

SPECIAL NOTES:

ALL 120 VOLT SINGLE PHASE, 15 AND 20AMPERE BRANCH CIRCUITS SUPPLYING OUTLETS INSTALLED IN DWELLING UNIT FAMILY ROOMS, DINING ROOMS, LIVING ROOMS, PARLORS ,LIBRARIES, DEN, BEDROOMS, SUNROOMS, RECREATION ROOMS , CLOSET, HALLWAYS, OR SIMILAR ROOMS OR AREAS SHALL BE PROTECTED AY A LISTED ARC-FAULT CIRCUIT INTERRUPTER, COMBINATION TYPE, INSTALLED TO PROVIDE PROTECTION OF THE BRANCH CIRCUIT PER NEC 210.12.
PROVIDE TAMPER RECEPTACLES AT ALL LOCATIONS WHERE THEY ARE MOUNTED NO HIGHER THAN 5-1/2 FEET AFF OR IN A SPACE DEDICATED TO A SPECIFIC APPLIANCE.

WWW.RANSOMSOLUTION.COM

CONFIDENTIAL CLIENT

SOUTH FLORIDA, FL

PORTFOLIO SAMPLE - CLIENT INFORMATION REMOVED

FIRE DAMAGE REPAIR

No.	Description	Date

Electrical Plans

Project number	RS-1053
Date	09/04/26
Drawn by	S.B.R.
Checked by	

E101

Scale DO NOT SCALE

SEAL REMOVED

PORTFOLIO SAMPLE

ENGINEER SEAL

Panel Tag- PANEL "A"

Panel Location-
Voltage (Phase-Ground/Phase-Phase) 120 240
Phase- 1
Rated Amps- 100
MCB 100
Wire- C
AIC- 10k
Mounting- Surface

Circuit	Description	New/ Existing	Load Type	Breaker Size	Poles	Wire Size	A	B	A	B	Wire Size	Poles	Breaker Size	Load Type	New/ Existing	Description	Circuit
1	LIGHTING		L	15	1	2#12+1#12G, 1/2"C	0.5		0.4		2#12+1#12G, MC	1	20*	R		RECEPTS - OUTDOOR	2
3	WATER HEATER		WH	20	2	3#12+1#12G, 1/2"C		1.5		0.5	2#12+1#12G, MC	1	20*	R		RECEPTS - LIVING	4
5	"		WH	"		"	1.5		0.2		2#12+1#12G, MC	1	20*	R		RECEPTS - BATH	6
7	A/C-1,2,3 & CU-1		MCA	25	2	3#10+1#10G, 3/4"C		2.3		0.1	2#12+1#12G, MC	1	20*	R		RECEPTS - KITCHEN	8
9	"		MCA	"		"	2.3		0.1		2#12+1#12G, MC	1	20*	R		RECEPTS - KITCHEN	10
11	SPACE		Space							0.7	2#12+1#12G, MC	1	20*	R		RECEPTS - REF	12
13	SPACE		Space						0.9		2#12+1#12G, MC	1	20*	R		GARBAGE DISPOSAL	14
15	SPACE		Space							2.5	3#8+1#10G, 3/4"C	2	40*	R		RECEPTS - RANGE	16
17	SPACE		Space						2.5		"		"	R		"	18
19	SPACE		Space							0.2	2#12+1#12G, MC	1	20*	R		EXHAUST FAN	20
21	SPACE		Space						1.5		2#12+1#12G, MC	1	20*	R		RECEPTS - DISHWASHER	22
23	SPACE		Space							0.6	2#12+1#12G, MC	1	20*	R		RECEPTS - BEDROOM # 1	24
25	SPACE		Space						0.6		2#12+1#12G, MC	1	20*	R		RECEPTS - BEDROOM # 2	26
27	SPACE		Space											Space		SPACE	28
29	SPACE		Space											Space		SPACE	30
							A	B	Total								
						Connected Load	10.5	8.4	18.9								
						Connected Amps	87.58	69.91	78.74								

*** PROVIDE ARC FAULT C/B**

LIGHTING FIXTURE SCHEDULE

SYMBOL	DESCRIPTION	MANUFACTURER	CATALOG NO.	LAMP NO.	LAMP TYPE	LAMP FIX. VOLTAGE	LAMP COLOR	LAMP CRI	LAMP LUMENS	FIXTURE WATTAGE	FINISH	MOUNTING	L/W
◎	6" DIAMETER ROUND RECESSED DOWNLIGHT	CREE LIGHTING	FIXTURE: CR6T-825L-35K-12-E26GU24 TRIM: CR6T-TRMSTAN-1	1	LED	120V	3500 °K	90	825	11 W	WHITE	RECESSED CEILING	
⋈	EXTERIOR WALL SCONCE	LITHONIA LIGHTING	FIXTURE: WST LED-P1-27K-VW-MVOLT-E20WC-DDBXD	1	LED	120V	2700 °K	80	1,500	12 W	BRONZE	SURFACE WALL MOUNTED	125
⋔	LED FAN LIGHT	HUNTER FAN	MODEL: ROMULUS WITH LED LIGHT	1	LED	120V	2700 °K	80	-	40 W	SILVER	SURFACE CEILING	
▽▽▽	BATHROOM VANITY LIGHT	KICHLER	MODEL: HENDRIK VANITY LIGHT 3-LIGHT	1	LED	120V	2700 °K	80	1,500	12 W	CHROME	SURFACE WALL MOUNTED	125

1. ALL LIGHTING FIXTURES TO BE APPROVED BY THE ARCHITECT PRIOR TO ORDERING AND INSTALLING.
2. ARCHITECT TO SELECT COLOR OF LIGHTING FIXTURES
3. REFER TO ARCHITECTURAL REFLECTED CEILING AND ELEVATION PLANS FOR EXACT LOCATION AND MOUNTING HEIGHT.
4. LISTED FOR INSTALLATION IN RATED FLOOR-CEILING ASSEMBLIES.
5. A MINIMUM OF 75 PERCENT OF THE LAMPS IN PERMANENTLY INSTALLED LIGHTING FIXTURES SHALL BE HIGH -EFFICACY LAMPS.

LAMP	EFFICIENCY
15WATTS	40 LUMENS PER WATTS
15W-40W	50 LUMENS PER WATTS
40W OR MORE	60 LUMENS PER WATTS

6. EXTERIOR LIGHTING SHALL COMPLY WITH THE REQUIREMENTS OF TABLE 4093.2 FOR THE EXTERIOR LIGHTING ZONE (LZ) APPROPRIATE TO THE BUILDING SITE.
7. INTERNALLY ILLUMINATED EXIST SIGNS SHALL NOT EXCEED 5 WATTS PER SIDE.
8. IC RATED RECESSED LIGHTING FIXTURES SEALED AT HOUSING/INTERIOR FINISH AND LABELED TO INDICATE < OR EQUAL TO 2.0 CFM LEAKAGE AT 75 PA.

LOAD DEMAND CALCULATION DWELLING UNIT NEC


UNIT TYPE: UNIT A

LIGHTING/RECEPTACLE 600 @3W/SQ/FT	= 1800	WATTS
KITCHEN/SMALL APPLIANCES (2)(1500)	= 3000	
LAUNDRY	= 1500	
FIRST 3000VA AT 100%	= 3000	
REMAINDER AT 35%	= 1155	
GENERAL LOAD	= 4155	
Appliance Load		
DISHWASHER (01)	= 1500	
RANGE (01)	= 5000	
REFRIGERATOR (01)	= 700	
WATER HEATER (01)	= 3000	
DISPOSAL	= 900	
APPLIANCE LOAD 4 OR MORE @ 75%	= 11,100x0.75 = 8325	
GREATER LOAD -COOLING	= 4577	
25% OF LARGEST MOTOR	= 1144	
MISCELLANEOUS	= 500	
TOTAL	18,701	VA
TOTAL (240V,1PH)	78	AMPS
	EXISTING 100 AMP SERVICE IS ENOUGH	

FEEDER OR SERVICE LOAD OPTIONAL CALCULATION NEC TABLE 220.84

INCOMING SERVICE MAIN SWAD

METER CENTER # 1 @ 60,241 WATTS, PER UNITS	= 18,701	WATTS
TOTAL CONNECTED LOAD	= 18,701	WATTS
TOTAL DEMAND LOAD PER (NEC 220.84)	= 18,701	WATTS
AMPS @ 240 VOLT, 1Ø	= 78	AMPS
HOUSE PANEL LOAD	= --	AMPS
TOTAL	= 78	AMPS
MINIMUM DEMAND LOAD FOR ELECTRICAL SERVICE AMPS @ 240 VOLT, 1Ø	= 78 EXISTING 100 AMP SERVICE IS ENOUGH	AMPS

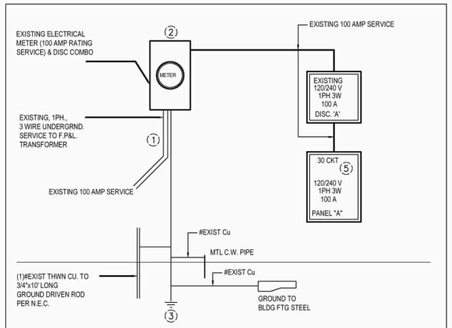

EXISTING 100 AMP SERVICE ELECTRICAL RISER DIAGRAM

NOTE: ELECTRIC SERVICE WILL BE INSTALLED @ 3' ABOVE MAIN FLOOD LEVEL

ELECTRICAL RISER NOTES: (#)

1. EXISTING SERVICE 100A, 120/240V, 1φ, 3W, FROM LOCAL AUTHORITY. V.I.F.
2. EXISTING UTILITY SERVICE CABINET 100A 120/240V, 1φ, 3W, V.I.F.
3. EXISTING GROUNDING PER NEC. V.I.F.
4. EXISTING TENANT PANEL 100MCB, 120/240V, 1φ, 3W, - SEE PANEL SCHEDULE.

ALL ELECTRICAL WIRING, BOXES, CONDUITS, RACEWAYS, CATV AND TELEPHONE WIRING PENETRATING FIRE RESISTANCE RATED MEMBRANCES MUST BE PROPERLY SEALED TO ASSURE THAT THE REQUIRED FIRE RATED RATING IS NOT REDUCE. UL 263 FIRE TESTS OF BUILDING CONSTRUCTION AND MATERIAL. SIMILAR TO ASTM E119 UL 1479 FIRE TESTS OF THROUGH-PENETRATION FIRESTOPS. COMPLEMENTARY TO UL 263. SIMILAR TO ASTM E 814

WWW.RANSOMSOLUTION.COM

CONFIDENTIAL CLIENT

SOUTH FLORIDA, FL

PORTFOLIO SAMPLE - CLIENT INFORMATION REMOVED

FIRE DAMAGE REPAIR

No.	Description	Date

Electrical Schedules

Project number	RS-1053
Date	09/04/26
Drawn by	S.B.R.
Checked by	
Scale	12" = 1'-0"

E102

SEAL REMOVED
PORTFOLIO SAMPLE

ENGINEER SEAL

GENERAL NOTES

A. GENERAL

1. THE CONTRACTOR SHALL COMPLY WITH LATEST EDITION OF NEC AND ALL APPLICABLE LOCAL CODES..
2. THE CONTRACTOR SHALL SECURE AND PAY FOR ALL PERMITS AND INSPECTIONS REQUIRED BY ANY OF THE FOREGOING AUTHORITIES, AND PAY FOR ALL OTHER COSTS IN CONNECTION WITH THE WORK. ALL CERTIFICATES SHALL BE IN DUPLICATE AND SHALL BE DELIVERED TO THE ARCHITECT/ENGINEER/OWNER.
3. THE SITE, LOCATION AND ROUTING OF SYSTEMS INDICATED TO HAVE NEW CONNECTIONS MADE TO THEM ARE SHOWN AS ACCURATELY AS FIELD CONDITIONS WOULD PERMIT. BIDDERS SHALL VISIT THE SITE AND THOROUGHLY EXAMINE THE CONTRACT DRAWINGS. BIDDERS WHO DO NOT VISIT THE SITE MAY BE UNILATERALLY NOT PERMITTED TO SUBMIT A BID IF THE OWNER SO DESIGNATES. ALL EXISTING CONDITIONS SHALL BE EXAMINED AND THEIR EXACT LOCATIONS VERIFIED. THE CONTRACTOR SHALL REPORT TO THE ARCHITECT/ENGINEER/OWNER BEFORE SUBMITTING A BID, ANY CONDITIONS WHICH MIGHT MAKE INSTALLATION OF REQUIRED EQUIPMENT A PROBLEM. NO CONSIDERATION OR ALLOWANCE WILL BE GRANTED FOR FAILURE TO INVESTIGATE CONDITIONS OR MISUNDERSTANDINGS OF THE CONTRACTUAL REQUIREMENTS.
4. THE CONTRACTOR SHALL REMOVE ALL EQUIPMENT NOT INDICATED TO BE REUSED TO A DESIGNATED LOCATION AT THE PROJECT SITE. AFTER THE EQUIPMENT HAS BEEN ASSEMBLED FOR THE OWNER'S INSPECTION AND POSSIBLE RETENTION, ALL EQUIPMENT NOT TO BE RETAINED BY THE OWNER SHALL BE REMOVED FROM THE SITE BY THE CONTRACTOR.
5. THE CONTRACTOR SHALL INSTALL AND CONNECT ALL EQUIPMENT AND MATERIALS IN ACCORDANCE WITH THE BEST ENGINEERING PRACTICE AND, UNLESS OTHERWISE SHOWN OR SPECIFIED, FOLLOW THE MANUFACTURER'S INSTRUCTIONS AND RECOMMENDATIONS AND FURNISH AND INSTALL ALL REQUIRED AUXILIARY ITEMS COMPLETE.
6. DRAWINGS SHALL BE CONSIDERED DIAGRAMMATIC AND FOR BIDDING PURPOSES ONLY. WHILE THE DRAWINGS ARE GENERALLY TO SCALE AND ARE AS ACCURATE AS THE SCALE WILL PERMIT, ALL IMPORTANT DIMENSIONS SHALL BE DETERMINED IN THE FIELD.
7. COORDINATE WITH ALL TRADES TO AVOID INTERFERENCE AMONG MECHANICAL, ELECTRICAL, ARCHITECTURAL AND STRUCTURAL ITEMS. PROVIDE ALL NECESSARY OFFSETS AND FITTINGS IN CIRCUITRY AND OTHER ITEMS REQUIRED TO INSTALL THE WORK WITHOUT INTERFERENCES.
8. THE CONTRACTOR SHALL TEST ALL EQUIPMENT INSTALLED UNDER THIS CONTRACT AND DEMONSTRATE TO THE OWNER ITS PROPER OPERATIONS. ALL NEW EQUIPMENT SHALL BE MOUNTED VIBRATION FREE.
9. ALL EQUIPMENT AND WORKMANSHIP SHALL BE GUARANTEED IN FULL FROM ALL DEFECTS FOR ONE (1) YEAR FROM THE DATE OF FINAL ACCEPTANCE OF THIS WORK.
10. ALL EQUIPMENT INSTALLED SHALL BE NEW AND SHALL CONFORM IN ALL RESPECTS TO THE LATEST APPROVED STANDARDS OF IEEE, ANSI, NEMA AND UNDERWRITERS LABORATORIES, INC., UNLESS INDICATED OTHERWISE.
11. REPAIR OF EXISTING WORK: ALL WORK SHALL BE CAREFULLY LAID OUT IN ADVANCE, AND WHERE CUTTING, CHANNELING, CHASING, OR DRILLING OF FLOORS, WALL, PARTITIONS, CEILINGS, OR OTHER SURFACES IS NECESSARY FOR THE PROPER INSTALLATION, SUPPORT, OR ANCHORAGE OF THE CONDUIT, RACEWAYS OR OTHER ELECTRICAL WORK, THIS WORK SHALL BE CAREFULLY DONE, AND ANY DAMAGE TO BUILDING, PIPING, OR EQUIPMENT SHALL BE REPAIRED BY SKILLED MECHANICS OF THE TRADE INVOLVED, AT NO ADDITIONAL COST TO THE OWNER. METHODS FOR AND EXACT LOCATIONS OF PROPOSED CUTTING, CHANNELING, CHASING OR DRILLING OF EXISTING CONSTRUCTION SHALL BE AS APPROVED BY THE OWNER.
12. THE CONTRACTOR SHALL REPAIR ALL WALL, CEILING, FLOOR, OR ROOF OPENINGS WHICH ARE CREATED BY DEMOLITION OR PENETRATION. THE REPAIRS SHALL BE WITH MATERIALS AND FINISHES TO MATCH EXISTING. ALL FIRE RATED PENETRATIONS SHALL BE SEALED WITH SUITABLE MATERIALS TO PRESERVE FIRE RATED INTEGRITY.
13. DEFINITIONS
    a. "PROVIDE" UNDER THIS CONTRACT IS DEFINED AS FURNISH AND INSTALL.
    b. "CONCEALED" UNDER THIS CONTRACT IS DEFINED AS WITHIN ARCHITECTURAL WALLS AND ABOVE CEILINGS.
    c. "EXPOSED" UNDER THIS CONTRACT IS DEFINED AS VISIBLE TO VIEW.
    d. "INDICATED" UNDER THIS CONTRACT IS DEFINED AS SHOWN IN THE CONTRACT DOCUMENTS.
    e. "CIRCUITRY" UNDER THIS CONTRACT IS DEFINED AS CONDUIT, FEEDER AND OR CIRCUIT.
15. UPON COMPLETION OF THE WORK, THE CONTRACTOR SHALL THOROUGHLY CLEAN THE CONTRACT AREA AND ALL OTHER AREAS USED FOR STORAGE, STAGING, ETC.
16. THE CONTRACTOR SHALL NOTIFY THE ARCHITECT/ENGINEER/OWNER WHEN THE PROJECT IS APPROXIMATELY 75% COMPLETED IN ORDER TO SCHEDULE A PRE-FINAL REVIEW OF CONSTRUCTION. NO WORK SHALL BE CONCEALED BY CEILINGS, WALLS, ETC. FINAL REVIEW SHALL BE SCHEDULED AT 100% COMPLETION. ALL PUNCH LIST ITEMS MUST BE ACCOMPLISHED PRIOR TO FINAL ACCEPTANCE.
17. PROVIDE TEMPORARY SERVICE FOR LIGHTING AND POWER EQUIPMENT (DRILLS, SAW, ETC.). VERIFY TEMPORARY REQUIREMENTS WITH GENERAL CONTRACTOR. TEMPORARY LIGHTING AND POWER SHALL MEET OSHA REQUIREMENTS AND LOCAL CODE. TEMPORARY POWER SHALL BE 120 VOLTS.
18. PROTECT ADJACENT MATERIALS INDICATED TO REMAIN. INSTALL AND MAINTAIN DUST AND NOISE BARRIERS TO KEEP DIRT, DUST, AND NOISE FROM BEING TRANSMITTED TO ADJACENT AREAS. REMOVE PROTECTION AND BARRIERS AFTER DEMOLITION OPERATIONS ARE COMPLETE.
19. FINAL TESTING: AT THE TIME OF FINAL INSPECTION AND TESTS, ALL CONNECTIONS AT PANELBOARDS, DEVICES AND EQUIPMENT AND ALL SPLICES MUST BE COMPLETED. EACH BRANCH CIRCUIT AND ITS RESPECTIVE CONNECTED EQUIPMENT MUST TEST FREE OF SHORT CIRCUITS. UPON COMPLETION OF THE WORK, CLEAN AND POLISH ALL EXPOSED SURFACES IN ACCORDANCE WITH THE MANUFACTURER'S RECOMMENDATIONS.
20. CONTRACTOR SHALL PROVIDE ACCESS PANEL FOR JUNCTION BOXES, DISCONNECT SWITCHES, OR OTHER DEVICES WHICH REQUIRE SERVICE ACCESS PER NEC.
21. SUBMIT COPIES OF SHOP DRAWINGS TO ARCHITECT FOR REVIEW. SUBMITTAL DATA MUST SHOW MANUFACTURER'S NAME, PUBLISHED RATINGS OR CAPACITY DATA AND OTHER PERTINENT DATA. SUBMITTALS ARE REQUIRED FOR BUT ARE NOT LIMITED TO THE FOLLOWING ITEMS:
    1) CIRCUIT BREAKERS AND PANELBOARDS
    2) LAMPS
    3) LIGHTING FIXTURES
    4) SAFETY SWITCHES
    5) WIRING DEVICES
22. PROVIDE AS BUILT DRAWINGS TO OWNER AT THE END OF THE CONSTRUCTION.

SPECIFICATIONS

RACEWAYS, BOXES AND CONDUITS

1. OUTDOORS WIRING METHODS: USE THE FOLLOWING WIRING METHODS:
    a. EXPOSED: CONDUCTORS IN RIGID METAL CONDUIT
    b. CONCEALED: CONDUCTORS IN RIGID METAL CONDUIT.
    c. UNDERGROUND: CONDUCTORS IN RIGID NONMETALLIC CONDUIT, UNLESS OTHERWISE NOTED.
    d. CONNECTION TO VIBRATING EQUIPMENT: CONDUCTORS IN LIQUID-TIGHT FLEXIBLE METAL CONDUIT.
    e. BOXES AND ENCLOSURES: NEMA TYPE 3R.
2. INDOORS WIRING METHODS: USE THE FOLLOWING METHODS:
    a. CONNECTION TO VIBRATING EQUIPMENT: CONDUCTORS IN FLEXIBLE METAL CONDUIT, EXCEPT IN WET OR DAMP LOCATIONS USE LIQUIDTIGHT FLEXIBLE METAL CONDUIT.
    b. DAMP OR WET LOCATIONS: CONDUCTORS IN RIGID STEEL CONDUIT.
    c. EXPOSED: CONDUCTORS IN ELECTRICAL METALLIC TUBING.
    d. CONCEALED: CONDUCTORS IN ELECTRICAL METALLIC TUBING OR, AS APPROVED, METAL-CLAD (MC) CABLE.
    e. BOXES AND ENCLOSURES: NEMA TYPE 1, EXCEPT IN DAMP OR WET LOCATIONS USE NEMA TYPE 4, STAINLESS STEEL.
3. ALL CIRCUITRY IN FINISHED AREAS SHALL BE RUN CONCEALED.
4. MINIMUM SIZE CONDUIT SHALL BE 1/2".
5. EMT CONNECTORS AND COUPLINGS SHALL BE OF THE ALL-STEEL, COMPRESSION TYPE WITH INSULATED THROAT.
6. EXPOSED AND CONCEALED CIRCUITRY (WHETHER CONDUIT AND WIRE OR CABLE) SHALL BE RUN TIGHT TO CEILING SLAB (AS HIGH AS POSSIBLE TO MAXIMIZE HEADROOM) IN A NEAT, WORKMANLIKE MANNER. ALL RUNS SHALL BE PARALLEL OR PERPENDICULAR TO BUILDING WALLS.
7. EXPOSED LOW VOLTAGE WIRING SHALL BE INSTALLED IN A RACEWAY, UNLESS OTHERWISE NOTED.
8. OUTLET BOXES SHALL BE A MINIMUM OF 4" SQUARE WITH THE APPROPRIATE PLASTER RING OR TILE COVER.
9. WHERE EXISTING WALLS ARE FURRED OUT AND DEVICES ARE NOT NOTED TO BE REMOVED, PROVIDE EXTENSION BOXES TO BRING FACE OF DEVICES FLUSH WITH NEW FINISH SURFACE AND CONTINUE IN SERVICE.

C. WIRE AND CABLE
1. ALL CONDUCTORS SHALL BE COPPER, MINIMUM #12 TYPE "THHN-THWN" INSULATION.
2. ALL WIRE SIZES SHALL BE AS NOTED AND COMPLY WITH NEC.
3. ALL "MC" CABLE SHALL HAVE AN INTERNAL GREEN INSULATED EQUIPMENT GROUND CONDUCTOR.
4. ALL 120 VOLT CIRCUIT HOMERUNS WHICH ARE OVER 100 LINEAR FEET SHALL BE #10 CONDUCTORS MINIMUM FOR THE ENTIRE CIRCUIT.

D. WIRING DEVICES AND TELEPHONE/CABLE OUTLETS
1. THE LOCATION OF ALL WIRING DEVICES AND TELEPHONE/DATA OUTLETS SHALL BE VERIFIED BEFORE INSTALLATION WITH THE ARCHITECT. THE ARCHITECT MAY RELOCATE ANY DEVICE 5 FEET AT NO CHARGE TO THE OWNER.
2. DEVICE PLATES SHALL BE A FINISH AND COLOR SELECTED BY THE ARCHITECT.
3. COORDINATE WALL MOUNTED TELEPHONE/CABLE OUTLET LOCATIONS WITH THE ARCHITECT. TELEPHONE/CABLE CONDUCTORS SHALL BE INSTALLED BY OTHERS.
4. INSTALL SUPPORTING DEVICES TO FASTEN ELECTRICAL COMPONENTS SECURELY AND PERMANENTLY IN ACCORDANCE WITH NEC REQUIREMENTS AND ANY ADDITIONAL LOCAL CODES.

F. ELECTRICAL IDENTIFICATION
1. APPLY EQUIPMENT IDENTIFICATION LABELS (MINIMUM 1" HIGH LETTERS) OF ENGRAVED PLASTIC-LAMINATE ON EACH MAJOR UNIT OF ELECTRICAL EQUIPMENT. APPLY LABELS FOR EACH UNIT OF THE FOLLOWING CATEGORIES OF ELECTRICAL:
    a. PANELBOARDS AND DISCONNECTS.
    b. ACCESS DOORS AND PANELS FOR CONCEALED ELECTRICAL ITEMS.

G. GROUNDING
1. GROUND ELECTRICAL SYSTEMS AND EQUIPMENT IN ACCORDANCE WITH NEC EXCEPT WHERE GROUNDING IN EXCESS OF NEC REQUIREMENTS IS INDICATED.
2. ALL CIRCUITS SHALL CONTAIN AN INSULATED GROUNDING CONDUCTORS. ALL NEW RECEPTACLE CIRCUITS SHALL CONTAIN A #12 INSULATED GROUNDING CONDUCTOR.
3. SEPARATELY DERIVED SYSTEMS REQUIRED BY NEC TO BE GROUNDED SHALL BE GROUNDED AS APPROVED BY THE AUTHORITY HAVING JURISDICTION.

I. PANELBOARDS
1. IN PANELBOARDS, "EQUIPPED SPACE" OR "SPACE" IS DEFINED TO INCLUDE ALL NECESSARY BUS, DEVICE SUPPORTS AND CONNECTIONS FOR INSERTION OF A FUTURE DEVICE.
2. PANELBOARD CIRCUITING SHALL MATCH THE DRAWINGS. CIRCUITING CHANGES MUST BE APPROVED BY THE ENGINEER.
3. PANELBOARD BUS SHALL BE COPPER WITH BOLT-ON BRANCH CIRCUIT BREAKERS.
4. BEFORE ORDERING PANELBOARDS, COORDINATE ALL MOTOR CIRCUIT BREAKER TRIPS WITH MECHANICAL EQUIPMENT MANUFACTURER'S REQUIREMENTS.
5. SURFACE MOUNTED PANELBOARD CABINETS SHALL BE INSTALLED ON AN APPROVED STEEL SLOTTED SUPPORT SYSTEM TO DISTRIBUTE THE WEIGHT EVENLY TO THE WALL AND FLOOR AND TO PROVIDE A 1-INCH AIR SPACE BETWEEN WALL AND CABINET.
6. FOR RECESSED PANELBOARDS, RUN ONE 3/4" CONDUIT FROM TOP OF PANEL 6" INTO CEILING SPACE FOR EVERY SET OF 3 SPARE CIRCUIT BREAKERS OR SPACES.
7. PANELBOARD SHALL BE EQUAL TO SQUARE D TYPE NEHB, NQOD, OR MANUFACTURED EQUIVALENT BY GENERAL ELECTRIC, EATON/CUTLER HAMMER, OR SIEMENS.
8. PROVIDE FRAMED, TYPED CIRCUIT DIRECTORY WITH EXPLICIT DESCRIPTION AND IDENTIFICATION OF ITEMS CONTROLLED BY EACH INDIVIDUAL BREAKER. PROVIDE NEW PANELBOARD DIRECTORY FOR ALL EXISTING AND NEW PANELBOARDS AFFECTED BY RENOVATION. PANELBOARD DIRECTORY SHALL BE REVISED TO REFLECT ALL REVISED FIELD CONDITIONS.

J. FUSES
4. INSTALL FUSES IN FUSIBLE DEVICES AS INDICATED.
5. INSTALL TYPEWRITTEN LABELS ON THE INSIDE DOOR OF EACH FUSED SWITCH TO INDICATE FUSE REPLACEMENT INFORMATION.

SPECIFICATIONS

K. DISCONNECTS AND CIRCUIT BREAKERS
1. ENCLOSED NON-FUSIBLE SWITCH SHALL BE NEMA HEAVY-DUTY TYPE WITH ENCLOSURE CONSISTENT WITH ENVIRONMENT WHERE LOCATED, HANDLE LOCKABLE WITH 2 PADLOCKS, AND INTERLOCKED WITH COVER IN "CLOSED" POSITION.
2. ENCLOSED FUSIBLE SWITCHES SHALL BE NEMA HEAVY-DUTY TYPE WITH CLIPS TO ACCOMMODATE SPECIFIED FUSES, ENCLOSURE CONSISTENT WITH ENVIRONMENT WHERE LOCATED, HANDLE LOCKABLE WITH 2 PADLOCKS AND INTERLOCKED WITH COVER IN "CLOSED" POSITION.
3. ENCLOSED MOLDED-CASE CIRCUIT BREAKER: FRAME SIZE, TRIP RATING, NUMBER OF POLES, AND AUXILIARY DEVICES AS INDICATED; INTERRUPTING CAPACITY RATING TO MEET AVAILABLE FAULT CURRENT, 10,000 SYMMETRICAL RMS AMPERES MINIMUM; WITH APPROPRIATE APPLICATION LISTING WHEN USED FOR SWITCHING FLUORESCENT LIGHTING LOADS OR HEATING, AIR CONDITIONING, AND REFRIGERATION EQUIPMENT.
4. ENCLOSURE: NEMA TYPE 1, UNLESS SPECIFIED OR REQUIRED OTHERWISE TO MEET ENVIRONMENTAL CONDITIONS OF INSTALLED LOCATION.
    a. OUTDOOR LOCATIONS: TYPE 12/3R.
    b. KITCHEN AREAS: TYPE 4X, STAINLESS STEEL.
    c. OTHER WET OR DAMP INDOOR LOCATIONS: TYPE 4.
6. PROPERLY SUPPORT DISCONNECT OR ENCLOSED CIRCUIT BREAKER ON WALL WITH METAL FRAMING AS REQUIRED.

M. LIGHTING
1. COORDINATE RECESSED LIGHTING FIXTURES WITH MECHANICAL EQUIPMENT AND ARCHITECTURAL CEILING PLAN. GRID LAYOUT ON PLANS IS APPROXIMATE. ADJUST LIGHTING FIXTURES IN FIELD PER ARCHITECT.
2. PROVIDE FINISHING FRAMES FOR ALL RECESSED LIGHTING FIXTURES, TYPE TO BE COMPATIBLE WITH CEILING. COORDINATE ALL FIXTURE TYPES WITH CEILING SYSTEM BEFORE ORDERING FIXTURES. PROVIDE ALL MOUNTING ATTACHMENTS FOR A COMPLETE INSTALLATION.
3. ALL NEW LIGHTING FIXTURES SHALL BE INSTALLED COMPLETE WITH LAMPS. SEE PLANS FOR SPECIFIC REQUIREMENTS. PROVIDE NEW LAMPS FOR ALL EXISTING LIGHTING FIXTURES.
4. FINISHES OF LIGHTING FIXTURES SHALL BE AS SELECTED BY THE ARCHITECT.

N. EQUIPMENT LOCATION
1. DO NOT INSTALL NEW PANELBOARDS, SWITCHBOARDS AND/OR MOTOR CONTROL CENTERS UNDERNEATH NEW OR EXISTING DUCTWORK AND/OR PIPING. IF SUCH CONDITIONS ARE ENCOUNTERED, NOTIFY THE ENGINEER FOR FURTHER EVALUATION AND DIRECTIVES. INSTALLING THE PANELBOARD IN A DIFFERENT LOCATION AGREED TO BY THE ENGINEER AND OWNER TO AVOID THIS SCENARIO SHALL BE AT SOLE COST TO THE CONTRACTOR.

O. DEMOLITION
1. PROVIDE DEMOLITION AS INDICATED ON DEMOLITION PLANS. CIRCUITRY NOTED FOR REMOVAL SHALL BE REMOVED BACK TO THE SOURCE BUS UNLESS OTHERWISE NOTED. CONTRACTOR SHALL BE RESPONSIBLE FOR THE COMPLETE REMOVAL FROM THE SITE FOR ALL EQUIPMENT AND MATERIAL REMOVED UNDER DEMOLITION WORK, UNLESS OTHERWISE NOTED OR DIRECTED. EXISTING CIRCUITS-TO-REMAIN INTERRUPTED BY DEMOLITION SHALL BE RESTORED FOR OPERATION AS BEFORE. OUTAGES REQUIRED TO PERFORM DEMOLITION SHALL BE COORDINATED WITH THE OWNER AND PROCESSED OUTSIDE OF NORMAL BUSINESS HOURS. REPAIR ALL WALL, CEILING, FLOOR OR ROOF OPENINGS CREATED BY DEMOLITION.
2. LOCATE, IDENTIFY AND PROTECT ELECTRICAL SERVICES PASSING THROUGH DEMOLITION AREA AND SERVING OTHER AREAS OUTSIDE THE DEMOLITION LIMITS. MAINTAIN SERVICES TO AREAS OUTSIDE DEMOLITION LIMITS. WHEN SERVICES MUST BE INTERRUPTED, INSTALL TEMPORARY SERVICES FOR AFFECTED AREAS.

ABBREVIATIONS

A	AMP	LTG	LIGHT	P	POLE
AFF	ABOVE FINISHED FLOOR	MFR	MANUFACTURER	PNL	PANEL
AIC	AMPERES INTERRUPTING CAPACITY(MIN)	MCB	MAIN CIRCUIT BREAKER	PH,ø	PHASE
CB	CIRCUIT BREAKER	MH	MOUNTING HEIGHT	(R)	REMOVE EXISTING AND RELOCATED
C	CONDUIT	MLO	MAIN LUG ONLY	(RE)	RELOCATED EQUIP.
CKT	CIRCUIT	N	NEUTRAL	RECPT	RECEPTACLE
EC	EMPTY CONDUIT	(N)	NEW ITEMS	TBD	TO BE DETERMINED
(E)	EXISTING TO REMAIN. CONT. IN SERVICE	NEC	NATIONAL ELECTRICAL CODE	UON	UNLESS OTHERWISE NOTED
FA	FIRE ALARM	NIC	NOT IN CONTRACT	V	VOLT
FLA	FULL LOAD AMPS	OEM	ORIGINAL EQUIPMENT MANUFACTURER	W	WIRE
G	GROUND	OFCI	OWNER FURNISHED CONTRACTOR INSTALLED	W/	WITH
HP	HORSE POWER			WP	WEATHERPROOF
KVA	KILO-VOLT AMPERE			XFMR	TRANSFORMER
KW	KILOWATT			(X)	REMOVE WITH ALL CIRCUITRY THERETO

ELECTRICAL SYMBOLS

DESIGNATION	DESCRIPTION	MTG HGT TO CENTERLINE AFF (UON)
	INCANDESCENT, COMPACT FLUORESCENT OR LED LIGHTING FIXTURE "A" (IF SHOWN) INDICATES FIXTURE TYPE AND "a" (IF SHOWN) INDICATES SWITCH CTRL	–
	INCANDESCENT, COMPACT FLUORESCENT OR LED WALL WASHER TYPE LIGHTING FIXTURE "A" (IF SHOWN) INDICATES FIXTURE TYPE. "a" (IF SHOWN) INDICATES SWITCH CONTROL	–
S	SINGLE POLE TOGGLE SWITCH. MOUNTING HEIGHT +48" A.F.F., U.O.N. SUBSCRIPTS AT SWITCH SYMBOL INDICATE THE FOLLOWING: OS – WALL MOUNTED OCCUPANCY SENSOR, SIMILAR TO WATTSTOPPER CAT. # DSW-100, DSW-200(FOR BI-LEVEL SWITCHING) OR EQUAL D – DIMMER, 1000W U.O.N. 3 – 3-WAY SWITCH a,b,c – IDENTIFICATION OF LIGHTS CONTROLLED K – LOCK TYPE	4'-0"
	AFCI DUPLEX RECEPTACLE: 20A-125V-2P, 3W. MOUNTING HEIGHT +18" A.F.F. UNLESS OTHERWISE NOTED. SUBSCRIPTS ADJACENT TO RECEPTACLE SYMBOL INDICATE THE FOLLOWING: WP – WEATHERPROOF GFI – GROUND FAULT INTERRUPTING IG – ISOLATED GROUND DED – DEDICATED CIRCUIT FL – FLOOR MOUNTED – RECESSED.	18"
	DEDICATED DUPLEX RECEPTACLE – NEMA 5-20R – ON SEPARATE CIRCUIT	18"
	DUPLEX RECEPTACLE – NEMA 5-20R WITH INTEGRAL GROUND FAULT CIRCUIT INTERRUPTER	18"
	SPECIAL PURPOSE SINGLE RECEPTACLE – SEE DRAWING FOR DESCRIPTION	18"
TV	TELEVISION – PROVIDE 4" SQUARE BOX AND STUB OUT 3/4" EC 6" INTO CEILING SPACE	REFER TO ARCH. UON
EC 1,3	HOMERUN TO PANELBOARD – NO. OF ARROWHEADS INDICATE NO. OF CIRCUITS. NUMERALS & LETTERS ADJACENT TO ARROWHEADS INDICATE ASSIGNED PANEL & CKT #	
▶	TELEPHONE OUTLET STUB OUT 1" EC 6" INTO CEILING SPACE WITH PLASTER RING AND PULL STRING TO ACCESSIBLE CEILING SPACE	REFER TO ARCH. UON
	GROUND	–
	PANELBOARD 120/240V SYSTEM	6'-0" TO TOP
M	MOTOR CONNECTION	–
30	NON-FUSED SAFETY DISCONNECT SWITCH – NUMERAL DENOTES SWITCH SIZE – 3 POLE UON	5'-0" TO TOP
60 40	FUSED SAFETY DISCONNECT SWITCH – UPPER NUMERAL DENOTES SWITCH SIZE, LOWER NUMERAL DENOTES FUSE SIZE – 3 POLE UON	5'-0" TO TOP
#10	TICK MARKS IN HOMERUN OR BRANCH CIRCUITRY, UNLESS OTHERWISE SCHEDULED, INDICATE THE QUANTITY (WHEN MORE THAN TWO) OF CURRENT CARRYING CONDUCTORS. NUMERAL ADJACENT TO TICKS INDICATES WIRE SIZE WHEN OTHER THAN #12 AWG. ALL WIRING SHALL ALSO CONTAIN AN INSULATED EQUIPMENT GROUND CONDUCTOR SIZED PER NEC. (NOT SHOWN)	
	GENERAL CIRCUITRY	
1	KEY NOTE, NEW WORK	
1	KEY NOTE, DEMOLITION	
	FACTORY CONNECTION – PROVIDE CIRCUITRY CONNECTION AS NOTED ON PLAN	
M	METER	–
	HALF SWITCHED RECEPTACLE, 18" A.F.F.	
J	JUNCTION BOX, WALL MOUNTED.	
U	UTILITY METERING.	
S	SMOKE DETECTOR W/ BATTERY. CONNECT AHEAD OF AN UNSWITCHED 120V CIRCUIT, DO NOT EXCEED 1500VA.	
CM	CARBON MONOXIDE SENSOR	

WWW.RANSOMSOLUTION.COM

CONFIDENTIAL CLIENT

SOUTH FLORIDA, FL

PORTFOLIO SAMPLE - CLIENT INFORMATION REMOVED

FIRE DAMAGE REPAIR

No.	Description	Date

Electrcial Notes & Specs


Project number	RS-1053
Date	09/04/26
Drawn by	S.B.R.
Checked by	

E103

Scale 12" = 1'-0"

SEAL REMOVED
PORTFOLIO SAMPLE

ENGINEER SEAL

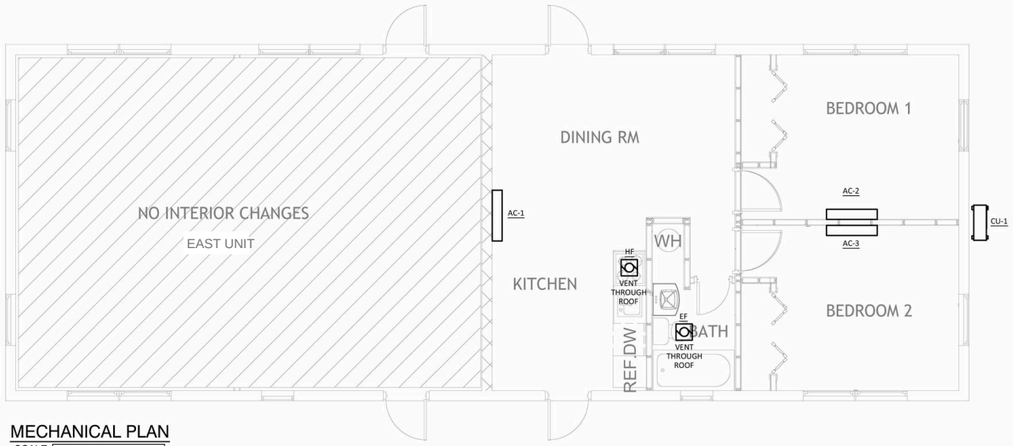

MECHANICAL PLAN

SCALE: N.T.S. - DO NOT SCALE

MECHANICAL NOTES

EQUIPMENT	DUCT SIZE	NOTES
EXHAUST FAN, EF	4"Ø	ROUTE TO EXTERIOR WALL/ROOF.
KITCHEN HOOD FAN, HF	7"Ø	ROUTE TO EXTERIOR WALL/ROOF.
INDOOR/OUTDOOR UNIT	-	REFRIGERANT PIPING ROUTE TO BE DETERMINED IN FIELD, SIZE PER MANUFACTURER REQUIREMENTS. ROUTE CONDENSATE DRAIN PIPE TO APPROVED OUTDOOR LOCATION OR GRAVITY DRAIN TERMINATION IN ACCORDANCE WITH FBC-MECHANICAL SECTION 307. PROVIDE DRAIN PAN UNDER UNIT.
THERMOSTAT	-	PROGRAMMABLE THERMOSTAT, 5° HEATING/COOLING DEADBAND. FOR HEAT PUMPS PROVIDE THERMOSTAT THAT HAS ABILITY TO AUTOMATICALLY DETECT AUX HEAT TEMPERATURE SETPOINT. SENSI MODEL ST75.


GENERAL NOTES

GENERAL NOTES:

1. EQUIPMENT HAS BEEN SIZED PER MANUAL J CALCULATIONS. SMALLEST SIZE AVAILABLE FROM THE MANUFACTURER HAS BEEN SELECTED.
2. SEE SPECIFICATIONS FOR DUCTWORK INSULATION R-VALUE, INSIDE AND OUTSIDE THE BUILDING.
3. MECHANICAL VENTILATION AND LOCAL EXHAUST SHALL COMPLY WITH FBC-RESIDENTIAL / MECHANICAL CHAPTER 4.
4. EXHAUST AIR OUTLETS SHALL TERMINATE AT LEAST 3 FT FROM PROPERTY LINES, 3 FT FROM OPERABLE OPENINGS INTO THE BUILDING, AND 10 FT FROM MECHANICAL OUTDOOR AIR INTAKES UNLESS LOCATED 3 FT ABOVE THE INTAKE.
5. PROVIDE BACKDRAFT DAMPERS ON ALL EXHAUST TERMINATIONS IN ACCORDANCE WITH CODE.
6. MECHANICAL PIPING SHALL BE INSULATED WITH R-3 INSULATION. PROVIDE ALUMINUM JACKET WHEN INSTALLED OUTDOORS FOR WEATHER PROTECTION.
7. PROVIDE PROGRAMMABLE THERMOSTATS WITH HEATING/COOLING DEADBAND.
8. TEMPERATURE CONTROLS SHALL HAVE SETPOINT OVERLAP RESTRICTIONS.

NOTE:

BATHROOMS CONTAINING A BATHTUB, SHOWER, OR TUB/SHOWER SHALL BE MECHANICALLY VENTED FOR HUMIDITY CONTROL

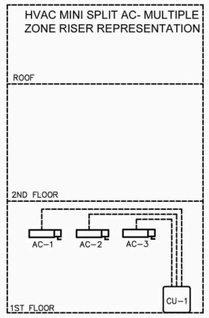

MINI SPLIT HEAT PUMP SCHEDULE

INDOOR UNIT									OUTDOOR UNIT					
MARK	SERVES	SUPPLY CFM	COOLING DATA			HEATING	V/PH	MCA/ MOCP	MARK	AMBIENT AIR TEMP °F	ELECTRICAL			BASIS OF DESIGN - DAIKIN
			TOTAL MBH	EAT °F		TOTAL MBH					V/PH	MCA	MOCP	
				DB	WB									
AC-1	LIVING/ KITCHEN	400	12	78	65	12	230/1	POWERED BY OUTDOOR UNIT	CU-1	95	208-230/1	19.9	25	DAIKIN MODEL: 3MXM24AVJU9 2-FTXV09AVJU9 FTXV12AVJU9 INDOOR UNIT AC-1: FTXV12AVJU9 AC-2 & AC-3: FTXV09AVJU9 OUTDOOR UNIT CU-1: 3MXM24AVJU9
AC-2	BEDROOM # 1	300	9	78	65	9	230/1							
AC-3	BEDROOM # 2	300	9	78	65	9	230/1							


1. EQUIPMENT CAPACITY SIZED IN ACCORDANCE WITH ACCA MANUAL J AND MANUAL S CALCULATIONS.
2. ROUTE CONDENSATE VIA GRAVITY SLOPE (MIN. 1/8" PER FOOT) TO APPROVED EXTERIOR DISCHARGE LOCATION (STORM DRAIN OR SPLASH PAD AT GRADE). PROVIDE INLINE CONDENSATE PUMP ONLY WHERE GRAVITY DRAINAGE IS NOT FEASIBLE. PROVIDE AUXILIARY FLOAT SWITCH PER FBC-M 307.
3. REFRIGERANT TYPE SHALL BE R-32.
4. PROVIDE CODE AND MANUFACTURER-REQUIRED CLEARANCES FOR ALL INDOOR AND OUTDOOR UNITS.
5. INSTALL INDOOR WALL HEADS AT MANUFACTURER-RECOMMENDED MOUNTING HEIGHTS.
6. CONTRACTOR SHALL CONFIRM REFRIGERANT LINE LENGTHS AND ELEVATION DIFFERENCES PRIOR TO ROUGH-IN. INSULATION SHALL BE MINIMUM R-4 (1/2" WALL) CLOSED-CELL ELASTOMERIC FOAM PROTECTED FROM UV OUTDOORS.
7. CONTRACTOR SHALL CONFIRM WITH MANUFACTURER THAT UNIT WILL PROVIDE SCHEDULED AIRFLOW TO EACH SPACE AT DESIGN STATIC PRESSURE.
8. PROVIDE OUTDOOR AIR VENTILATION DAMPER KIT WHERE REQUIRED BY LOCAL CODES (APRILAIRE MODEL 8125A OR APPROVED EQUAL).
9. SPACE DESIGN SETPOINTS: SUMMER 75°F DB, WINTER 70°F DB.

FAN SCHEDULE


NO.	SERVICE	TYPE	CFM	MAX SONES	V/PH	HP	MODEL
EF	EXHAUST FAN	CEILING EXHAUST	80	0.8	115/1	1/10	AIR KING FRAK80
HF	KITCHEN HOOD	DUCTED HOOD FAN	160	1.7	115/1	1/8	BROAN

NOTE:
OTHER MANUFACTURERS: FAN: EQUAL BY NUTONE, DELTA BREEZ
KITCHEN HOOD: EQUAL BY NUTONE, WHIRLPOOL


PROVIDE EXHAUST FAN FOR INSTALLATION IN FIRE RATED CEILING. DAMPER SHALL HAVE NON-ASBESTOS CERAMIC BLANKET, FUSIBLE LINK (165°F), UL LISTED 555C AND 263.

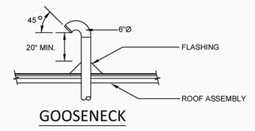


GOOSENECK

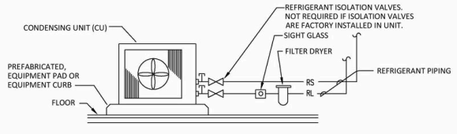


FLOOR MOUNTED CONDENSING UNIT

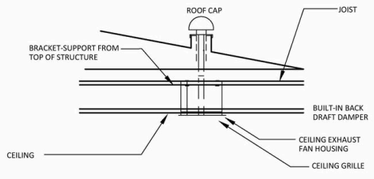

CEILING CABINET EXHAUST FAN DETAIL

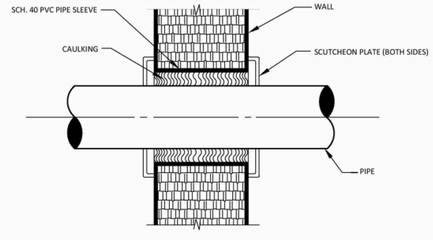

PIPE THRU WALL DETAIL

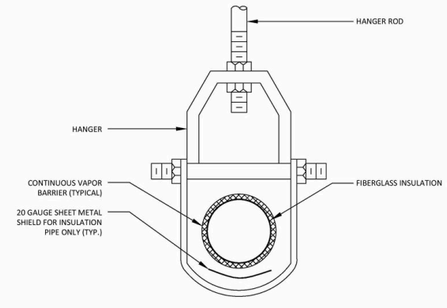

PIPE HANGER DETAIL

WWW.RANSOMSOLUTION.COM

CONFIDENTIAL CLIENT

SOUTH FLORIDA, FL

PORTFOLIO SAMPLE - CLIENT INFORMATION REMOVED

FIRE DAMAGE REPAIR

No.	Description	Date

Mechanical Plans

Project number	RS-1053
Date	09/04/26
Drawn by	S.B.R.
Checked by	

M101

Scale DO NOT SCALE

SEAL REMOVED
PORTFOLIO SAMPLE

ENGINEER SEAL

GENERAL NOTES

1. ALL WORK SHALL CONFORM TO ALL LOCAL AND STATE CODES, RULES AND REGULATIONS.

2. CONTRACTOR SHALL OBTAIN AND PAY FOR ALL PERMITS, FEES, AND TAXES AND OBTAIN, SCHEDULE, AND PAY FOR REQUIRED INSPECTIONS BY THE AUTHORITY HAVING JURISDICTION (AHJ). SCHEDULE AND CONDUCT INSPECTIONS REQUIRED BY AHJ TO OBTAIN FINAL CERTIFICATE OF OCCUPANCY (COO). INSPECTIONS AND APPROVALS BY THE AHJ ARE REQUIRED IN ADDITION TO ANY INSPECTIONS OR REVIEWS BY THE ARCHITECT AND ENGINEER. POST AND COMPLETE FORMS ASSOCIATED WITH THE PERMITS AND REQUIRED TO BE SIGNED BY THE AHJ. PROVIDE WRITTEN NOTIFICATION TO THE ARCHITECT AT LEAST TWO DAYS PRIOR TO EACH INSPECTION BY AHJ TO ALLOW FOR THE ARCHITECT OR ENGINEER TO OBSERVE THE INSPECTION.

3. MAKE NO CHANGES WITHOUT THE WRITTEN PERMISSION FROM THE ENGINEER.

4. ALL MATERIAL AND EQUIPMENT INDICATED ON THE PLANS AND DESCRIBED IN THE SPECIFICATIONS SHALL BE PROVIDED BY THE CONTRACTOR NEW AND THE BEST PRODUCTS OF REPUTABLE MANUFACTURERS AND SHALL BE IN NEW CONDITION AT ACCEPTANCE OF WORK.

5. THIS CONTRACTOR SHALL GUARANTEE ALL MATERIALS, LABOR AND EQUIPMENT FOR A PERIOD OF ONE YEAR FROM DATE OF ACCEPTANCE. COMPRESSORS SHALL HAVE A FULL FIVE-YEAR WARRANTY. CONTRACTOR SHALL PAY FOR ANY REPAIRS OR REPLACEMENTS CAUSED BY DEFECTIVE WORKMANSHIP OR FAULTY MATERIALS AS CONSTRUED HEREIN WITHIN THE PERIOD COVERED BY THE GUARANTEE.

6. SCAFFOLDING, RIGGING AND HOISTING: UNLESS OTHERWISE SPECIFIED, CONTRACTOR SHALL FURNISH ALL SCAFFOLDING, RIGGING, HOISTING, AND SERVICES NECESSARY FOR ERECTION AND DELIVERY INTO THE PREMISES OF ANY EQUIPMENT AND APPARATUS FURNISHED, AND REMOVAL OF SAME FROM PREMISES WHEN NO LONGER REQUIRED.

7. LOCATION OF EQUIPMENT, PIPING, AND OTHER MECHANICAL WORK IS INDICATED DIAGRAMMATICALLY BY THE DRAWINGS. DETERMINE EXACT LOCATIONS ON THE JOB SITE, SUBJECT TO STRUCTURAL CONDITIONS AND WORK OF OTHER CONTRACTORS.

8. CONTRACTOR ASSUMES RESPONSIBILITY FOR PROPER ARRANGEMENT OF PIPES, DUCTS, ETC., TO CONNECT APPROVED EQUIPMENT IN A PROPER AND APPROVED MANNER. FOLLOW EQUIPMENT MANUFACTURER'S DETAILED INSTRUCTIONS AND THE CONTRACT DOCUMENTS. NOTIFY THE ARCHITECT BEFORE PROCEEDING. NO EQUIPMENT INSTALLATION OR CONNECTIONS SHALL BE MADE IN A MANNER THAT VOIDS THE MANUFACTURER'S WARRANTY.

9. SEE ARCHITECTURAL DRAWINGS FOR THE LOCATION OF ROOF PENETRATIONS.

10. UNLESS OTHERWISE NOTED, ALL SPECIFIED EQUIPMENT IS LESS THAN 200 POUNDS. SEE ARCHITECTURAL DRAWINGS FOR SUPPORT DETAILS OF ALL EQUIPMENT GREATER THAN 200 LBS.

11. INSTALL EACH ITEM OF EQUIPMENT IN STRICT ACCORDANCE WITH MANUFACTURER'S RECOMMENDATIONS.

12. INSTALL ALL WORK IN A NEAT AND WORKMANLIKE MANNER, USING ONLY WORKMEN THOROUGHLY QUALIFIED IN THE TRADE OF DUTIES THEY ARE TO PERFORM. ROUGH WORK WILL BE REJECTED.

13. CUTTING AND PATCHING SHALL BE DONE BY THE APPROPRIATE TRADE UNLESS OTHERWISE REQUIRED BY TRADE CUSTOM OR SPECIFIED UNDER ANOTHER SECTION OF THE SPECIFICATIONS. CONTRACTOR SHALL FURNISH SKETCHES SHOWING THE LOCATIONS AND SIZES OF ALL OPENINGS, CHASES, ETC. REQUIRED. CONTRACTOR IS LIABLE FOR CUTTING OR PATCHING MADE NECESSARY BY HIS FAILURE TO MAKE PROPER ARRANGEMENTS IN THIS RESPECT.

14. DO NOT CUT STRUCTURAL MEMBERS WITHOUT THE APPROVAL OF THE ARCHITECT AND ALL SUCH CUTTING SHALL BE DONE IN A MANNER AS DIRECTED BY THEM.

15. MAINTAIN WORK AREA CLEAN AT ALL TIMES DURING CONSTRUCTION. AFTER COMPLETING INSTALLATIONS OF DUCTWORK, CONTRACTOR SHALL CLEAN ENTIRE SYSTEM OF RUBBISH, PLASTER, DIRT AND ANY OTHER DEBRIS.

16. TEST ALL SYSTEMS. SYSTEMS SHALL OPERATE SATISFACTORILY AS DESIGNED AND INTENDED. REPORT ANY DEFICIENCIES TO ARCHITECT.

SHOP DRAWINGS
1. CONTRACTOR SHALL SUBMIT SHOP DRAWINGS FOR THE FOLLOWING MATERIALS AND EQUIPMENT:

A. ALL HEATING AND COOLING EQUIPMENT
B. REFRIGERANT DRIERS, INDICATORS, SIGHT-GLASS AND RECEIVER WHEN NOT PART OF PACKAGED EQUIPMENT.
C. VALVES AND PIPING SPECIALTIES
D. PIPE AND DUCT INSULATION
E. FANS
F. AIR DEVICES
G. WALL AND ROOF CAPS
H. CONCENTRIC VENTS
I. TEMPERATURE CONTROLS
J. TESTING AND BALANCING REPORTS
K. OPERATION AND MAINTENANCE MANUALS

2. MECHANICAL CONTRACTOR SHALL BE RESPONSIBLE FOR COORDINATION OF MECHANICAL EQUIPMENT, DUCTWORK ROUTING, LOCATION OF SYSTEM COMPONENTS, AND ELECTRICAL REQUIREMENTS WITH THE ELECTRICAL CONTRACTOR. CONTRACTOR ORIGINATED MODIFICATIONS TO THE MECHANICAL EQUIPMENT ELECTRICAL INSTALLATION, DUE TO DEVIATIONS FROM THE MECHANICAL EQUIPMENT'S "BASIS OF DESIGN" OR "PROTOTYPE" ELECTRICAL DATA, SHALL BE AT A COST TO THE MECHANICAL CONTRACTOR.

GENERAL NOTES

EQUIPMENT

1. GENERAL:
REFER TO EQUIPMENT SCHEDULES FOR ADDITIONAL REQUIREMENTS.

2. AIR DEVICES:
STEEL CONSTRUCTION WITH ENAMEL FINISH, COLOR AS APPROVED BY OWNER/ARCHITECT.
ACCEPTABLE MANUFACTURERS: HARTY & COOLEY, TITUS, PRICE, AND NAILOR.

3. FANS:
EACH FAN SHALL BE AMCA CERTIFIED AND LABELED.
EACH FAN SHALL BE UL LISTED AND LABELED.
ALL WIRING PROVIDED AS PART OF THE UNIT SHALL BE IN ACCORDANCE WITH NEC.
ACCEPTABLE MANUFACTURERS: BROAN, COOK, GREENHECK OR PENN.
SUBMIT SAMPLE MODEL FOR ARCHITECTURAL REVIEW AND APPROVAL.
FAN EFFICACY SHALL BE MINIMUM 2.8CFM/W.

4. AIR HANDLING UNITS:

PACKAGED, FACTORY ASSEMBLED, PRE-WIRED AND PRE-PIPED WITH MICROPROCESSOR CONTROL SYSTEM AND ALL OPTIONS AS SCHEDULED. UL LISTED. AIR HANDLER LEAKAGE MUST BE DESIGNED BY MANUFACTURER AT LESS THAN OR EQUAL TO 2% OF AIR FLOW.
ACCEPTABLE MANUFACTURERS: COMFORTMAKER, TRANE, GOODMAN, OR YORK.

5. MINI-SPLIT UNITS:
INDOOR UNITS SHALL BE WALL MOUNTED OR DUCTED ABOVE CEILING.
MOUNT CONDENSING UNIT ON ROOF OR ON GRADE.
CONFIRM REFRIGERANT PIPE LENGTH WITH MANUFACTURER PRIOR TO PURCHASE.
PROVIDE EQUIPMENT SUPPORT. PROVIDE CONDENSATE DRAIN PUMP.
ACCEPTABLE MANUFACTURERS: LG, DAIKIN, FUJITSU, MITSUBISHI.

DUCTWORK

1. GENERAL: CONSTRUCT ALL DUCTWORK AND ACCESSORIES IN ACCORDANCE WITH THE LATEST EDITION OF SMACNA STANDARDS FOR 2" PRESSURE CLASS AND SEAL CLASS B.

2. METAL DUCTWORK: UNLESS OTHERWISE NOTED, FABRICATE ALL DUCTWORK, HOUSING, DAMPERS, AND ALL OTHER DUCT RELATED ACCESSORIES FROM GALVANIZED STEEL SHEETS. EXHAUST DUCTWORK AND ACCESSORIES SERVING SHOWER ROOMS SHALL BE CONSTRUCTED FROM ALUMINUM SHEETS.

A. GALVANIZED STEEL SHEETS: LOCK-FORMING QUALITY; COMPLYING WITH ASTM A 653/A 653M. G90 GALVANIZED COATING.
B. GALVANIZED SHEETS: ASTM B 209/B 209M, ALLOY 3003, TEMPER H14; WITH MILL FINISH FOR CONCEALED DUCTS AND STANDARD, 1-SIDE BRIGHT FINISH FOR EXPOSED DUCTS.

3. INSTALL ALL DUCTWORK ABOVE CEILING AND HOLD TIGHT TO UNDERSIDE OF STRUCTURE ABOVE UNLESS OTHERWISE INDICATED.

4. ALL ROUND RUNOUTS DUCTWORK TO A SINGLE CEILING DIFFUSER SHALL BE SAME SIZE AS DIFFUSER NECK.

5. INSTALL OUTSIDE AIR INTAKES, INCLUDING CONCENTRIC VENTS, A MINIMUM OF 10'-0" FROM ANY EXHAUST OR PLUMBING VENT.

6. INSTALL CEILING AIR DEVICES AS CLOSE AS POSSIBLE TO LOCATION SHOWN ON PLAN. COORDINATE LOCATION WITH LIGHT FIXTURES AND SPRINKLER HEADS.

7. HOLD ALL DUCTWORK RUNNING PARALLEL TO A RATED WALL A MINIMUM OF 6" AWAY FROM THE WALL.

8. CHANGES TO DUCT DUE TO FIELD CONDITIONS SHALL BE MADE ONLY IF THE DUCT SIZE FREE AREA IS MAINTAINED AND SHALL BE SUBMITTED TO ENGINEER FOR APPROVAL.

9. FLEXIBLE CONNECTORS: PROVIDE FLEXIBLE CONNECTORS AT THE INLET AND OUTLET CONNECTION FOR EACH FAN AND AIR HANDLING UNIT. EACH FLEXIBLE CONNECTOR SHALL ALLOW 1" OF FREE MOVEMENT AND SHALL BE COMPLETELY AIR TIGHT. PROVIDE NEOPRENE COATED GLASS FABRIC MATERIAL, MINIMUM 30 OZ. PER SQUARE YARD. CONTRACTOR SHALL BRACE DUCTWORK (AS REQUIRED) AT ALL FLEXIBLE CONNECTORS TO ENSURE THAT DUCTWORK IS KEPT IN ALIGNMENT.

MECHANICAL SPECIFICATIONS

LEAKAGE TEST:

A. ALL EXPOSED DUCT JOINTS SHALL BE SEALED WITH HARDCAST 601.
B. LEAKAGE TESTING FOR ALL DUCTWORK SHALL BE AS FOLLOWS:

THE TOTAL DUCT LEAKAGE SHALL BE = 4 CFM/100FT² WITH AIR HANDLER INSTALLED. A WRITTEN REPORT OF THE RESULTS OF THE TEST SHALL BE SIGNED BY THE PARTY CONDUCTING THE TEST AND PROVIDED TO THE CODE OFFICIAL UPON REQUEST. THE TEST SHALL BE PERFORMED IN THE PRESENCE OF THE OWNER'S REPRESENTATIVE.

C. PERFORM ALL TESTING AFTER THE SEALS HAVE CURED COMPLETELY AND BEFORE COVERING WITH INSULATION OR CONCEALING IN MASONRY.
ALL DUCT JOINTS ABOVE CEILING SHALL BE SEALED WITH MASTIC.

BLOWER TEST:
FOR ALL LEVEL 3, GUT REHAB OR NEW CONSTRUCTION: BLOWER DOOR TEST MUST BE CONDUCTED AT 50 Pa LESS THAN OR EQUAL TO 5 CHANGES PER HOUR.

PIPING

1. CONDENSATE DRAIN PIPING: TYPE SCHEDULE 40 PVC PIPING WITH GLUE TYPE FITTINGS. SLOPE ALL CONDENSATE PIPING TOWARDS DRAIN AT 1/8" PER FOOT.

2. REFRIGERANT PIPING: TYPE ACR HARD COPPER WITH STREAMLINE FITTINGS JOINTED WITH SPECIAL REFRIGERATION SOLDER SUCH AS SIL-FOS. RUN, SIZE, AND TRAP REFRIGERANT LINES PER MANUFACTURER'S RECOMMENDATIONS. REFRIGERANT PIPING IN CONCEALED LOCATIONS MAY BE ANNEALED SOFT TEMPERED ACR TUBING ASSEMBLED WITH "STAYBRITE NO. 8" SOLDER, PIPE, PIPE FITTINGS AND COMPONENTS SHALL BE CAPABLE OF WITHSTANDING THE PRESSURES AND TEMPERATURES OF THE SERVICE THEY ARE HANDLING. PRE-CHARGED OR PREFABRICATED LINES BY EQUIPMENT MANUFACTURER MAY BE USED. TUBING, USED FOR REFRIGERANT SERVICE SHALL BE CLEANED, SEALED, CAPPED OR PLUGGED PRIOR TO BEING SHIPPED FROM THE MANUFACTURER'S PLANT.

3. IDENTIFICATION: ALL PIPING SHALL BE IDENTIFIED BY NAME AND DIRECTIONAL FLOW ARROWS IN ACCORDANCE WITH ASME AND ANSI STANDARDS.

4. FINAL DRAIN AND REFRIGERANT LINES SHALL NOT BLOCK SERVICE ACCESS TO FAN OR AIR FILTER REMOVAL AT THE AHU.

PIPING SPECIALTIES

1. PROVIDE TRAPS FOR CONDENSATE DRAIN LINES AT ALL HVAC EQUIPMENT THAT IS NOT INTERNALLY TRAPPED.

INSULATION

1. ALL DUCT AND PIPE INSULATION AND COVERINGS SHALL HAVE A FIRE AND SMOKE HAZARD RATING AS TESTED UNDER PROCEDURE ASTM-E-84, NFPA 255 AND UL 723 NOT EXCEEDING A FLAME SPREAD RATING OF 25 AND A SMOKE DEVELOPED RATING OF 50.

2. SUPPLY AIR DUCTWORK SHALL BE INSULATED WITH A MINIMUM, INSTALLED R-VALUE OF 6.0.
SUPPLY AND RETURN AIR DUCTS LOCATED OUTSIDE THE BUILDING ENVELOPE AND IN ATTIC/UNCONDITIONED SPACES
SHALL BE INSULATED WITH A MINIMUM, INSTALLED R-VALUE OF 8.0.

3. PIPING: INSULATE ALL HEATING AND COOLING SYSTEM PIPING THAT CONVEYS FLUIDS THAT HAVE A DESIGN OPERATING RANGE OF LOWER THAN 55 DEGREES F OR GREATER THAN 105 DEGREES F. INSULATION SHALL HAVE A CONDUCTIVITY NOT EXCEEDING 0.27 BTU PER INCH/HR*FT2*DEGREE F AT 75 DEGREE F MEAN TEMPERATURE..

A. REFRIGERANT SUCTION: (OUTSIDE BUILDING) FOR PIPING SIZES 1-1/2" OR LESS, INSULATE WITH 1" THICK
ARMAFLEX FIRE RATED INSULATION OR APPROVED ON EQUAL, WITH ALL JOINTS SEALED WITH ARMAFLEX
ADHESIVE FOR PIPING SIZES GREATER THAN 1-1/2", INSULATION SHALL BE 1-1/2" THICK. WHERE POSSIBLE,
INSULATION SHALL BE SLIPPED OVER THE TUBING AS FULL CYLINDER. INSULATION OF PIPING SHALL
BE VAPOR TIGHT AND CONTINUOUS THROUGH HANGERS, WALLS, ETC. PROVIDE GALVANIZED SHEET METAL SADDLES AT HANGERS. OUTDOOR INSULATION SHALL BE COVERED WITH CONTINUOUS ALUMINUM
JACKET CLAMPED AND SEALED TO WITH STAND ALL WEATHER CONDITIONS.

B. REFRIGERANT LIQUID AND HOT GAS PIPING WITHIN THE BUILDING: INSULATE WITH 1/2" THICK ARMAFLEX FIRE RATED INSULATION OR APPROVED EQUAL.

4. INSULATION OR DUCTWORK AND PIPING PASSING THROUGH NON-RATED WALLS SHALL BE CONTINUOUS THROUGH THE WALL PENETRATION.

5. WHEREVER PIPES, DUCTWORK OR OTHER ITEMS PASS THROUGH FIRE RATED WALLS AND FLOORS, THE CONTRACTOR SHALL ADEQUATELY FIRE STOP THE SPACE BETWEEN THE ITEMS AND THE MASONRY OR THE SPACE BETWEEN THE ITEM AND SLEEVE. FIRE STOP SHALL BE A NON-COMBUSTIBLE, NON-MELTING, APPROVED MATERIAL.

6. RETURN DUCT SHALL BE SOUNDLINED WITH 1" SOUNDLINING.

MECHANICAL SPECIFICATIONS

MECHANICAL ACCESSORIES:
1. ACCESS PANELS: PROVIDE ACCESS PANELS IN DUCTWORK IN A LOCATION TO SERVICE DAMPERS. ACCESS PANELS SHALL BE OF THE INSULATED DOOR TYPE ON ALL INSULATED DUCTS AND SHALL NOT BE COVERED BY DUCT INSULATION. ACCESS PANELS SHALL BE CONSTRUCTED AND INSTALLED IN ACCORDANCE WITH SMACNA STANDARDS. MINIMUM SIZE OF ACCESS PANELS SHALL BE 12" X 12" EXCEPT WHERE DUCT IS LESS THAN 14" WIDE IN WHICH CASE ONE DIMENSION SHALL BE 12" AND THE OTHER SHALL BE 2" LESS THAN THE DUCT WIDTH. ACCESS DOOR SHALL BE ACCESSIBLE.
2. GRAVITY AND AUTOMATIC DAMPERS: PROVIDE GRAVITY BACKDRAFT/AUTOMATIC DAMPERS IN ALL OA AND EA DUCTS. DAMPERS SHALL OPEN WHEN OA OR EA FLOW AND SHALL CLOSE WHEN NOT IN USE. COORDINATE WITH ELECTRICAL FOR POWER REQUIREMENTS. PROVIDE ACCESS DOOR FOR SERVICE.
3. VOLUME DAMPERS: PROVIDE VOLUME DAMPERS IN ALL DUCT TAKEOFFS FROM THE MAIN SUPPLY AND RETURN AIR DUCT. PROVIDE VOLUME DAMPERS IN ALL BRANCH DUCTS TO REGISTERS AND GRILLES FOR BALANCING. INSTALL DAMPERS VIBRATION FREE.
4. FIRE DAMPERS; PROVIDE FIRE DAMPERS WHERE SHOWN ON DRAWINGS. DAMPERS SHALL BE UL LISTED. PROVIDE ACCESS FOR SERVICE.
5. TURNING VANES: PROVIDE TURNING VANES IN DUCTWORK PER SMACNA STANDARDS.
6. FLEXIBLE CONNECTORS: PROVIDE FLEXIBLE CONNECTION BETWEEN HVAC EQUIPMENT AND DUCTWORK TO PREVENT VIBRATION.

TEST AND BALANCING

11. SCOPE:

J. AN INDEPENDENT CONTRACTOR WITH NEBB OR AABC CERTIFICATION SHALL PROVIDE ALL LABOR, MATERIALS, EQUIPMENT, SERVICES AND PERFORM ALL OPERATIONS REQUIRED FOR COMPLETE BALANCING OF THE MECHANICAL SYSTEMS AND RELATED WORK AS INDICATED ON THE DRAWINGS AND SPECIFIED HEREIN.
K. BALANCING SHALL NOT BE PERFORMED UNTIL ALL MECHANICAL EQUIPMENT IS PROPERLY INSTALLED AND IS 100% OPERATIONAL; ALL TEMPERATURE CONTROLS ARE INSTALLED AND CALIBRATED AND ALL SYSTEMS ARE CLEANED, PIPING AND STRAINERS FLUSHED, AND CLEAN FILTERS INSTALLED.
L. IT IS THE INTENT OF THIS SPECIFICATION TO ENSURE THAT THE ENTIRE PROJECT IS SUBSTANTIALLY COMPLETE SO THAT ALL COMPONENTS OF ALL MECHANICAL SYSTEMS CAN BE PUT INTO NORMAL OPERATION WITH ALL WINDOWS AND DOORS CLOSED AND BALANCED IN THAT CONDITION, IN NO CASE IS THE CONTRACTOR TO PERFORM HIS WORK IN PIECEMEAL FASHION.

2. QUALITY ASSURANCE: SUBMIT TO OWNER THREE (3) COPIES OF BALANCING AND TESTING RECORDS SPECIFIED HEREIN SHOWING THE MECHANICAL SYSTEMS HAVE BEEN BALANCED AND ARE DELIVERING SPECIFIED QUANTITIES.

3. EACH PIECE OF EQUIPMENT SHALL BE IDENTIFIED AS TO LOCATION, SERVICE, MANUFACTURER AND MODEL NUMBER. THIS INFORMATION SHALL BE RECORDED AND INCLUDED IN THE FINAL BALANCE REPORT.

4. AFTER ADJUSTMENTS ARE COMPLETED, THE MECHANICAL SYSTEMS SHALL BE TESTED, AND THE FOLLOWING INFORMATION RECORDED AND INCLUDED IN THE FINAL BALANCE REPORT:

A. AIR HANDLING UNITS:

1) BLOWER RPM
2) MOTOR FULL LOAD AMPS
3) VOLTAGE
4) AIR FLOW – TOTAL
5) AIR FLOW – OUTSIDE AIR
6) AIR FLOW – RETURN AIR
7) STATIC PRESSURE – SUCTION
8) STATIC PRESSURE – DISCHARGE
9) STATIC PRESSURE – TOTAL
10) ENTERING AIR TEMPERATURE (DB) HEATING AND COOLING
11) LEAVING AIR TEMPERATURE (DB) HEATING AND COOLING
12) ENTERING AIR TEMPERATURE (WB) COOLING
13) LEAVING AIR TEMPERATURE (WB) COOLING

B. AIR DEVICES:

1) EACH AIR DEVICE SHALL BE IDENTIFIED AS TO LOCATION AND SERVICE
2) SIZE, TYPE AND MANUFACTURER OF AIR DEVICE LISTED
3) REQUIRED CFM AND TEST RESULTANT CFM EACH DEVICE

C. FANS:

1) TOTAL AIR FLOW
2) EXTERNAL STATIC PRESSURE
3) MOTOR FULL LOAD AMPS
4) VOLTAGE

D. CONDENSING UNITS AND AIR COOLED CONDENSERS:

1) COMPRESSOR FULL LOAD AMPS
2) FAN FULL LOAD AMPS
3) VOLTAGE
5. AFTER THE SYSTEMS HAVE BEEN BALANCED AND ALL ADJUSTMENTS COMPLETED, RUN EACH SYSTEM THROUGH A COMPLETE HEATING AND COOLING CYCLE BY ADJUSTING SET POINTS TO DETERMINE IF SYSTEM IS RESPONDING TO TEMPERATURE CONTROLS. RECORD THE SET POINTS USED, AND TIME FOR THE SPACE TO REACH SET POINTS FOR EACH MODE OF OPERATION. INCLUDE THERMOSTAT TEMPERATURE READING, AND AN INDEPENDENT TEMPERATURE MEASUREMENT AT EACH THERMOSTAT WHILE TESTING EACH MODE OF OPERATION. PROVIDE RESULTS IN TESTING AND BALANCING REPORT.

TEMPERATURE CONTROL

1. THERMOSTAT LOCATIONS SHOWN ARE APPROXIMATE AND SHALL BE COORDINATED WITH ARCHITECTURAL DRAWINGS. MOUNT THERMOSTATS 4'-0" ABOVE FINISHED FLOOR, UNLESS OTHERWISE NOTED.
2. PROVIDE INITIAL SETUP AND PROGRAMMING OF ALL CONTROLS AND DEMONSTRATE TO OWNER.
3. CONTROL WIRING LOCATED IN PLENUM SPACE NOT INSTALLED IN CONDUIT SHALL BE PLENUM RATED CABLE.
4. FOR CIRCULATING HOT WATER SYSTEMS PROVIDE ACCESSIBLE MANUAL CONTROLS.

HVAC LEGEND

SYMBOL	DESCRIPTION
12x6(E)	EXISTING DUCTWORK, EQUIPMENT OR PIPING TO REMAIN
12x6	EXISTING DUCTWORK, EQUIPMENT OR PIPING TO BE REMOVED OR RELOCATED
12x6	NEW OR RELOCATED DUCTWORK, EQUIPMENT OR PIPING
	DUCTWORK WITH SOUNDLINING
	SUPPLY DUCT TURNING UP
	RETURN/EXHAUST DUCT TURNING UP
	SUPPLY DUCT TURNING DOWN
	RETURN/EXHAUST DUCT TURNING DOWN
	TRANSITION IN DUCT, SQUARE TO SQUARE
	TRANSITION IN DUCT, SQUARE TO ROUND
	SQUARE THROAT DUCT ELBOW WITHOUT TURNING VANES
	SQUARE THROAT DUCT ELBOW WITH TURNING VANES
	RADIUS ELBOW
	45 DEGREE TAP
	SPIN-IN RUNOUT FITTING WITH BALANCING DAMPER AND FLEXIBLE DUCT
	CONICAL TAP
	FLEXIBLE DUCT
	FLEXIBLE DUCT CONNECTION
	RECTANGULAR SUPPLY AIR DIFFUSER
	RETURN AIR GRILLE
T	THERMOSTAT
	EXHAUST FAN
	SIDE WALL/DUCT REGISTER
125	CFM DESIGNATION SYMBOL & QUANTITY

ABBREVIATIONS

(E)	EXISTING TO REMAIN	IN WG	INCHES OF WATER GAUGE
(R)	EXISTING TO BE REMOVED AND RELOCATED	KW	KILOWATTS
(RE)	RELOCATED EQUIPMENT	LAT	LEAVING AIR TEMPERATURE
AC	AIR CONDITIONING UNIT	LBS	POUNDS
AFF	ABOVE FINISHED FLOOR	LRA	LOCKED ROTOR AMPS
AHU	AIR HANDLING UNIT	LWT	LEAVING WATER TEMPERATURE
BTUH	BRITISH THERMAL UNITS PER HOUR	MBH	THOUSAND BRITISH THERMAL UNITS PER HOUR
CFM	CUBIC FEET PER MINUTE	MCA	MINIMUM CIRCUIT AMPACITY
CG	CEILING GRILLE	MIN	MINIMUM
CR	CEILING REGISTER	MOCP	MAXIMUM OVER-CURRENT PROTECTION
DB	DRY BULB TEMPERATURE	OA	OUTSIDE AIR
DN	DOWN	PD	PRESSURE DROP
EAT	ENTERING AIR TEMPERATURE	PH	PHASE
EF	EXHAUST FAN	PSI	POUNDS PER SQUARE INCH
ESP	EXTERNAL STATIC PRESSURE	RA	RETURN AIR
EWB	ENTERING WET BULB TEMPERATURE	RH	RELATIVE HUMIDITY
EWT	ENTERING WATER TEMPERATURE	RLA	RUNNING LOAD AMPS
°F	DEGREES FAHRENHEIT	RPM	REVOLUTIONS PER MINUTE
FG	FLOOR GRILLE	SA	SUPPLY AIR
FR	FLOOR REGISTER	SL	SOUND LINING
FLA	FULL LOAD AMPS	SWR	SIDEWALL REGISTER
FT	FOOT, FEET	SWG	SIDEWALL GRILLE
GPM	GALLONS PER MINUTE	TYP	TYPICAL
HP	HORSEPOWER	V	VOLT, VOLTS
HZ	HERTZ (CYCLES PER SECOND)	WB	WET BULB TEMPERATURE
IN	INCH, INCHES	WG	WATER GAUGE
		WMS	WIRE MESH SCREEN

WWW.RANSOMSOLUTION.COM

CONFIDENTIAL CLIENT

SOUTH FLORIDA, FL
PORTFOLIO SAMPLE - CLIENT INFORMATION REMOVED

FIRE DAMAGE REPAIR

No.	Description	Date

Mechanical Notes & Specs

Project number	RS-1053
Date	09/04/26
Drawn by	S.B.R.
Checked by	

M102

Scale DO NOT SCALE

SEAL REMOVED
PORTFOLIO SAMPLE

ENGINEER SEAL